



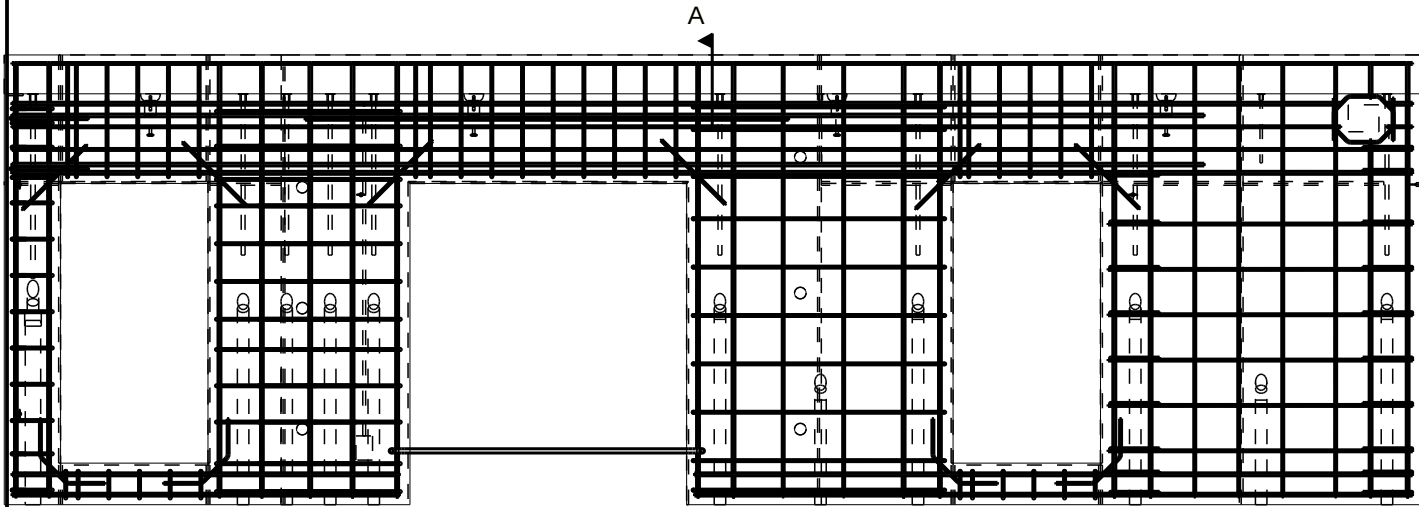

TOP IN FORM
1:50

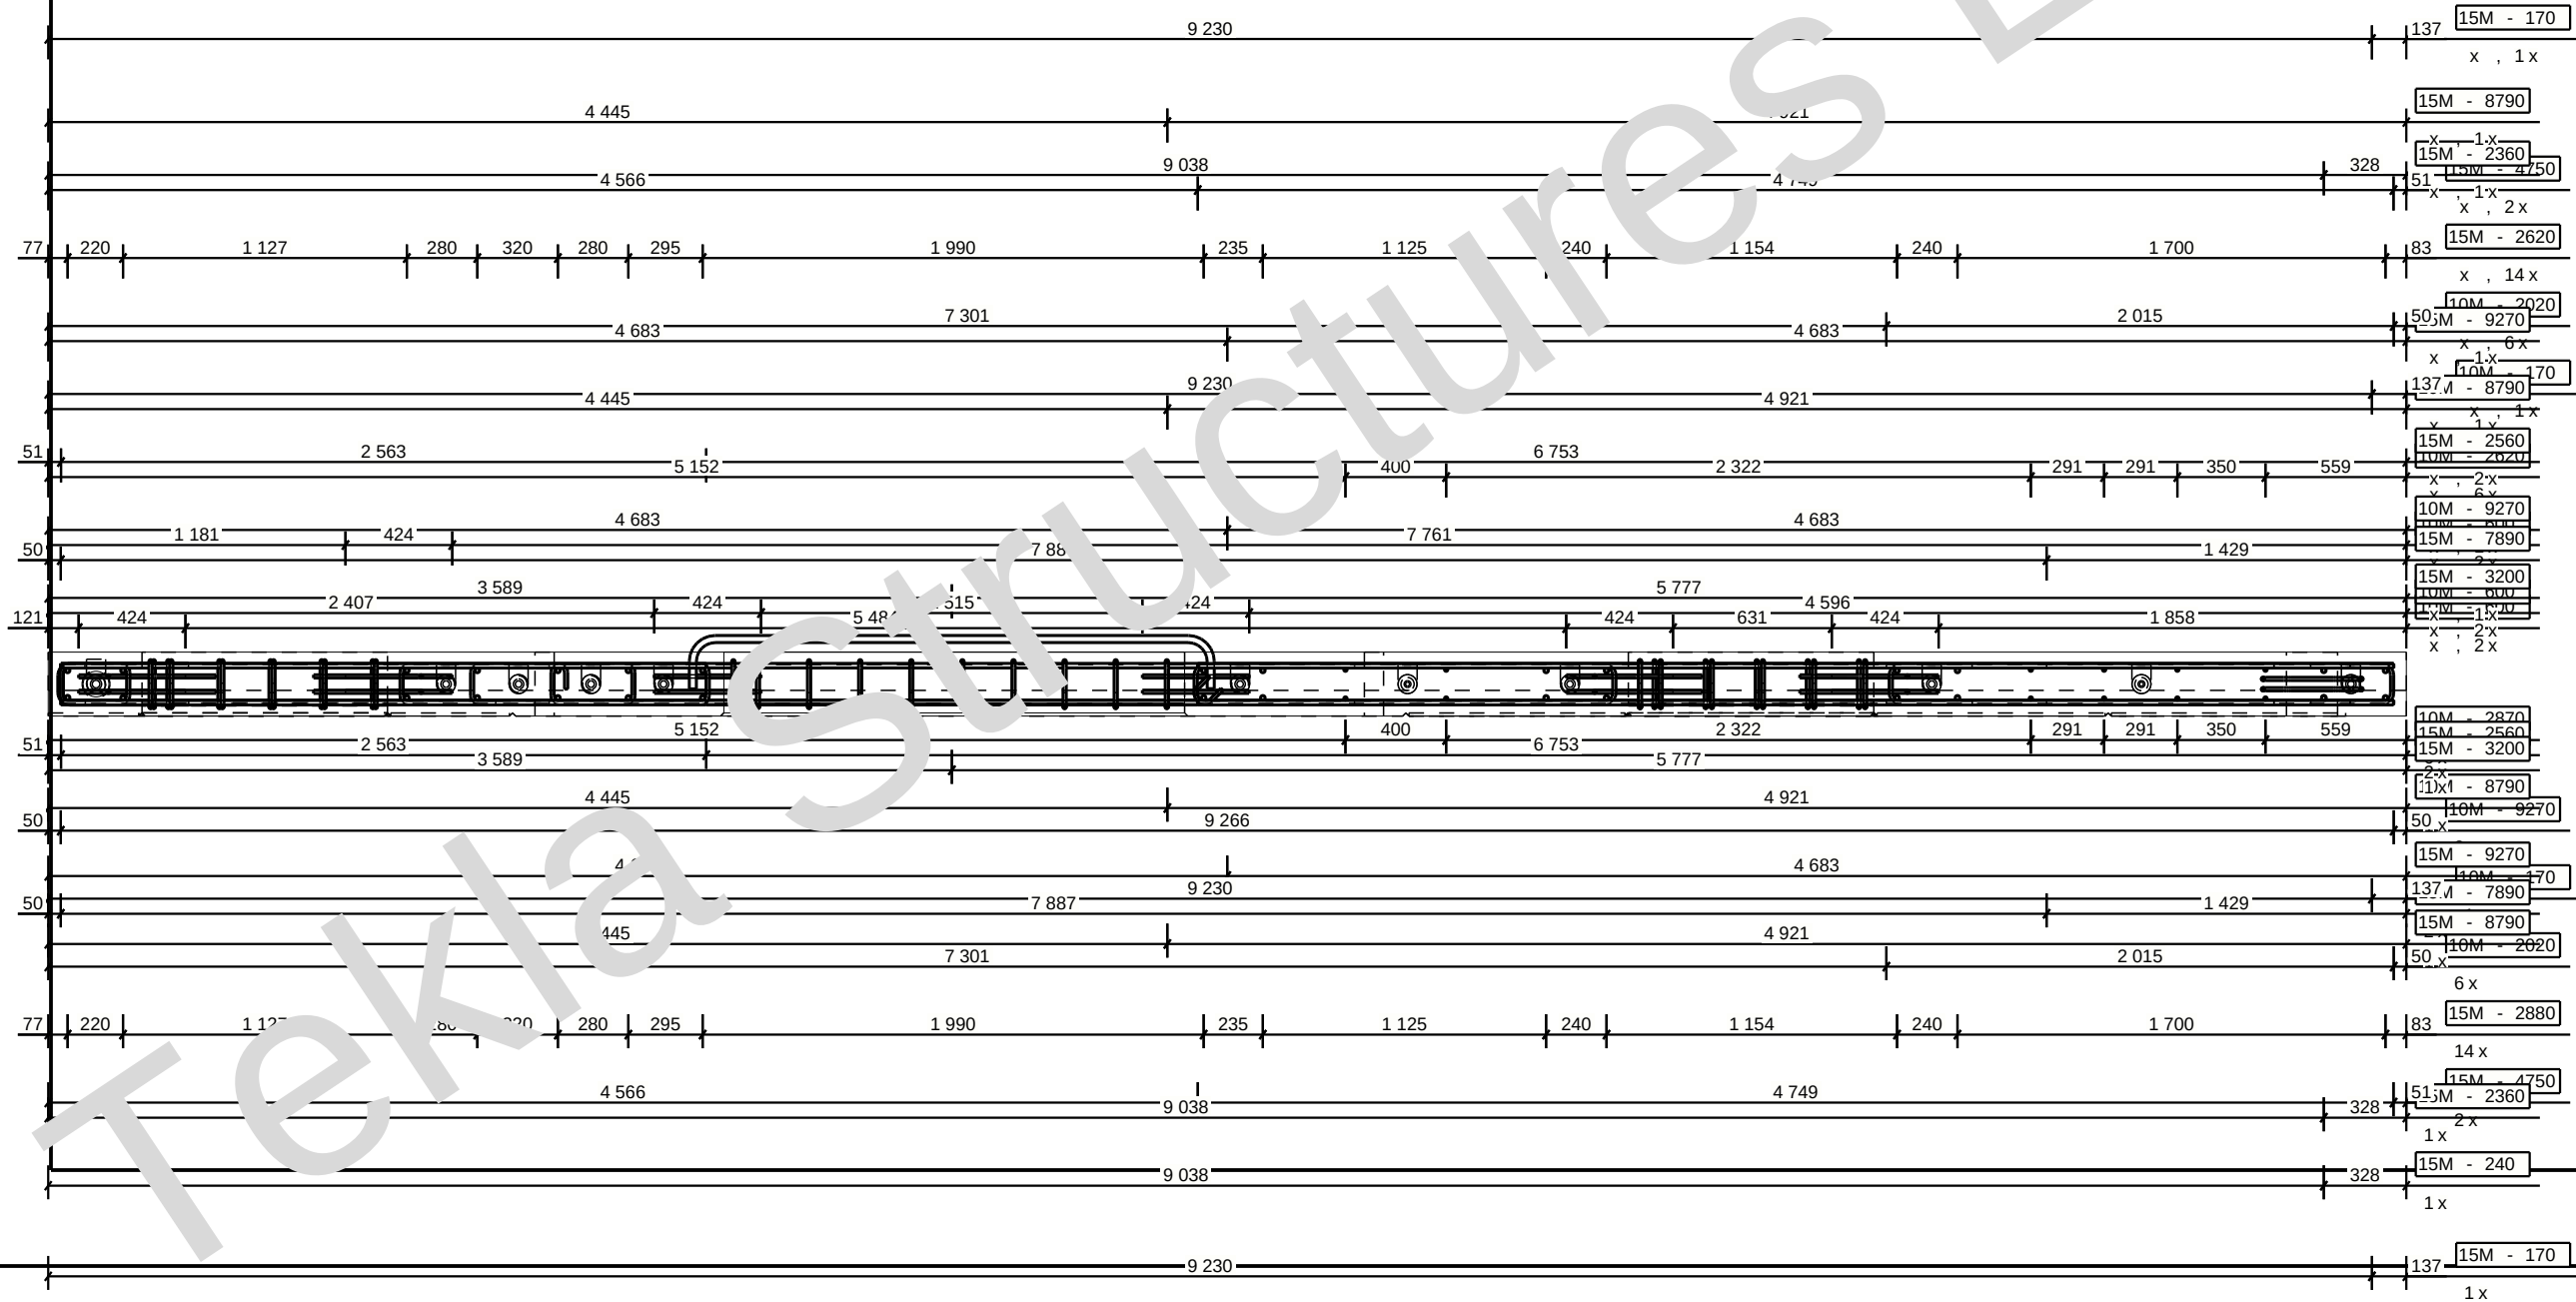

VIEW END 2
1:30

MARK	QTY.	DESCRIPTION	LENGTH	AREA
RB10M 0001	1	10M - 17	3790	
RB10M 0002	19	10M - 17	760	
RB10M 0003	12	10M - T1	890	
RB10M 0004	12	10M - Unknown	4240	
RB10M 0005	8	10M - TS5_1	750	
RB10M 0006	13	10M - TS67_2	1090	
RB10M 0007	4	10M - 14	860	
RB10M 0008	22	10M - Unknown	16910	
RB10M 0009	2	15M - Unknown	114	
RB10M 0010	2	15M - 17	2380	
RB10M 0011	2	10M - STR	170	
RB10M 0012	12	10M - STR	600	
RB10M 0013	12	10M - STR	2020	
RB10M 0014	6	10M - STR	2620	
RB10M 0015	6	10M - STR	2870	
RB10M 0016	2	10M - STR	8790	
RB10M 0017	3	10M - STR	9270	
RB10M 0018	14	15M - STR	2880	
RB10M 0019	2	15M - STR	3200	
RB10M 0020	4	15M - STR	4750	
RB10M 0021	4	15M - STR	7890	
RB10M 0022	2	15M - STR	8790	
RB10M 0023	2	15M - STR	9270	

VIEW A
1:30

STUBBE'S PRECAST		
PROJECT: PAISLEY TOWER		
PROJECT CODE: PTR	PAINT CODE:	UNITS REQD.: 1
DRAWN BY:	DATE: 22.09.2026	SCALE: AS SHOWN
ENGINEER:	DATE:	FILE:
PROJECT No: P22-132	PIECE MARK: W10-67 PAGE - 2	