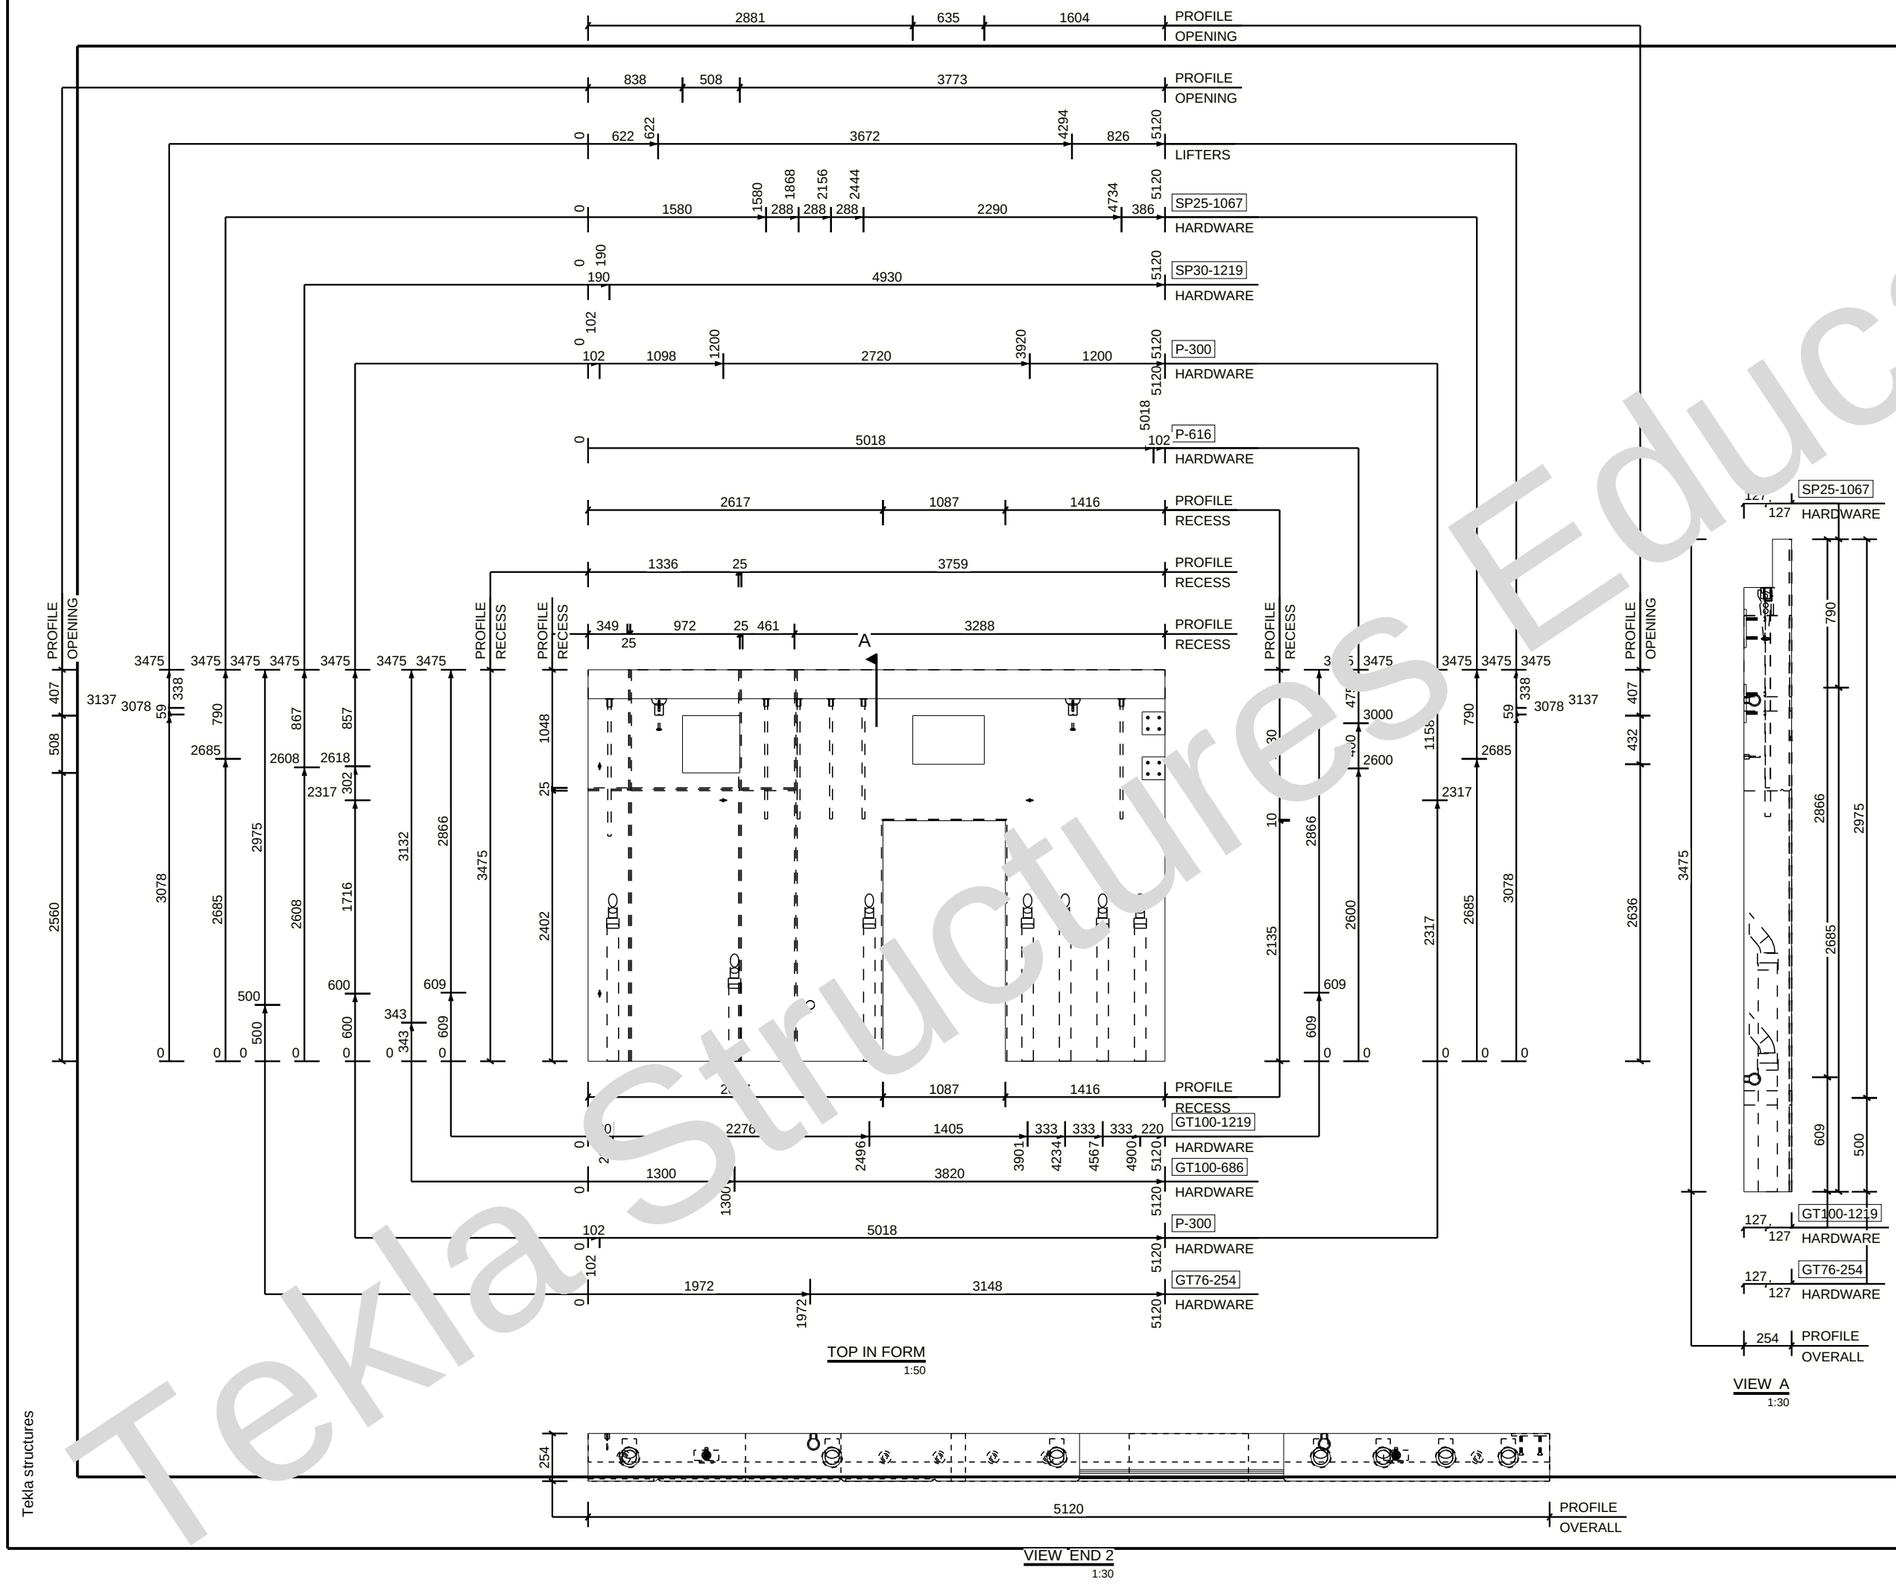


GENERAL NOTES

1) 28 DAY (MPa)	0
2) STRIPPING (MPa)	0
3) WEIGHT (LBS)	18317
4) AIR ENTRAINMENT	4% TO 7%
5) MIN COVER	25 mm
CLASS	F2
7) CONCRETE VOLUME (yd³)	4.53

CHARACTER	B	T	E	FINISH/NOTES
TROWEL SIDE				SCREED
FORM SIDE				
END 1				
END 2				
SIDE A				
SIDE B				

BILL OF MATERIALS

MARK No.	DESCRIPTION	QTY.
P-205	12000LB FORGED ANCHOR	2
GT76-254	76Ø x 254mm G.TUBE	1
GT100-686	100Ø x 686 GROUT TUBE	1
GT100-1219	100Ø x 1219 GROUT TUBE	6
P-300	19Ø INSERT (NC)	4
P-616	13x203x203 PLATE	2
SP25-1067	SP25Mx1067 WILLIAMS S	5
SP30-1219	30Mx1219 WILLIAMS SPL	1

NO.	DATE	DESCRIPTION	BY

STUBBE'S PRECAST

PROJECT: PAISLEY TOWER

PROJECT CODE:	PAINT CODE:	UNITS REQD.:
PTR		1
DRAWN BY:	DATE: 22.09.2026	SCALE: AS SHOWN
ENGINEER:	DATE:	FILE:

PROJECT No: P22-132

PIECE MARK: W10-78 PAGE - 1

Tekla structures

Tekla Structures Educational