



VIEW END 2
1:75

GENERAL NOTES			
1) 28 DAY (MPa)			0
2) STRIPPING (M)			0
3) WEIGHT (KGS)			24822
4) AIR CONTENT (%)			4% TO 7%
5) MIN COVER			25 mm
6) CLASS			F2
7) CONCRETE VOLUME (yd³)			6.05
CHARACTER	B	T	E
TROWEL SIDE			
FORM SIDE			
END 1			
END 2			
SIDE A			
SIDE B			
BILL OF MATERIALS			
MARK No.	DESCRIPTION	QTY.	
P-205	12000LB FORGED ANCHOR	4	
GT75-686	75Ø x 686 GROUT TUBE	2	
GT75-1219	75Ø x 1219 GROUT TUBE	8	
GT76-254	76Øx254mm G.TUBE	6	
GT100-1219	100Øx1219 GROUT TUBE	1	
P-300	19Ø INSERT (NC)	5	
P-602	13PL. W/STUD	1	
SP15-457	15Mx457 WILLIAMS SPL	2	
SP25-1067	SP25Mx1067 WILLIAMS S	8	
SP30-1219	30Mx1219 WILLIAMS SPL	1	
CNDT	19MM CONDUIT	1	
EB-S-PL	Single Plastic Electr	1	
NO.	DATE	DESCRIPTION	BY
STUBBE'S PRECAST			
PROJECT:			
PAISLEY TOWER			
PROJECT CODE:	PAINT CODE:	UNITS REQD.:	
PTR		1	
DRAWN BY:	DATE:	SCALE:	
	02.10.2026	AS SHOWN	
ENGINEER:	DATE:	FILE:	
PROJECT No:		PIECE MARK:	
P22-132		PAGE - 2	

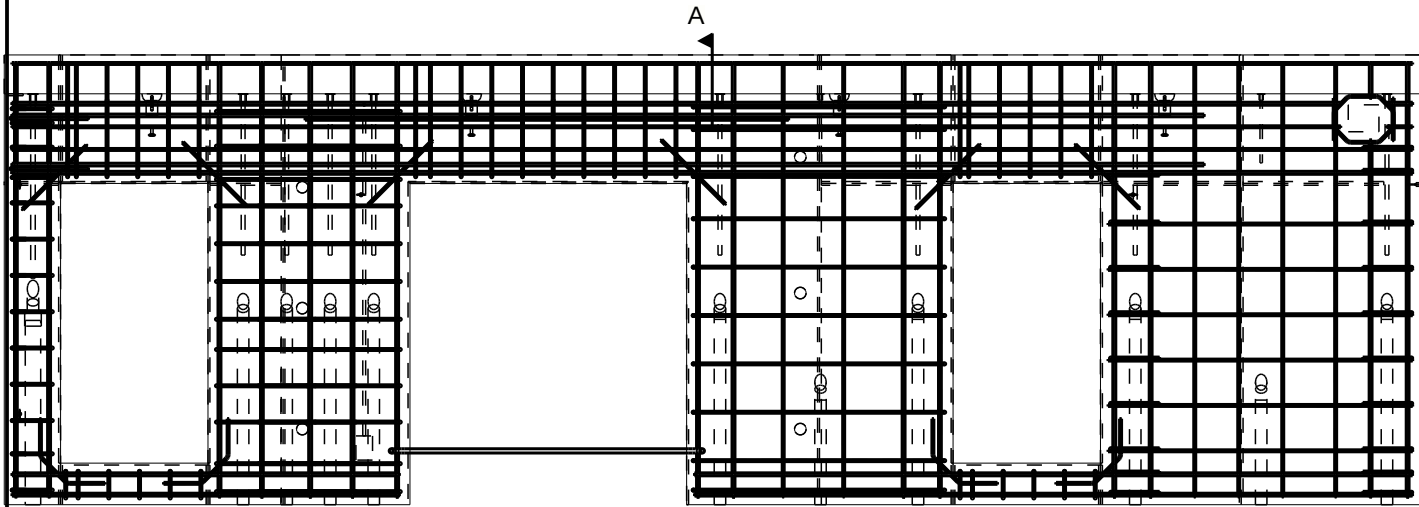













TOP IN FORM
1:50

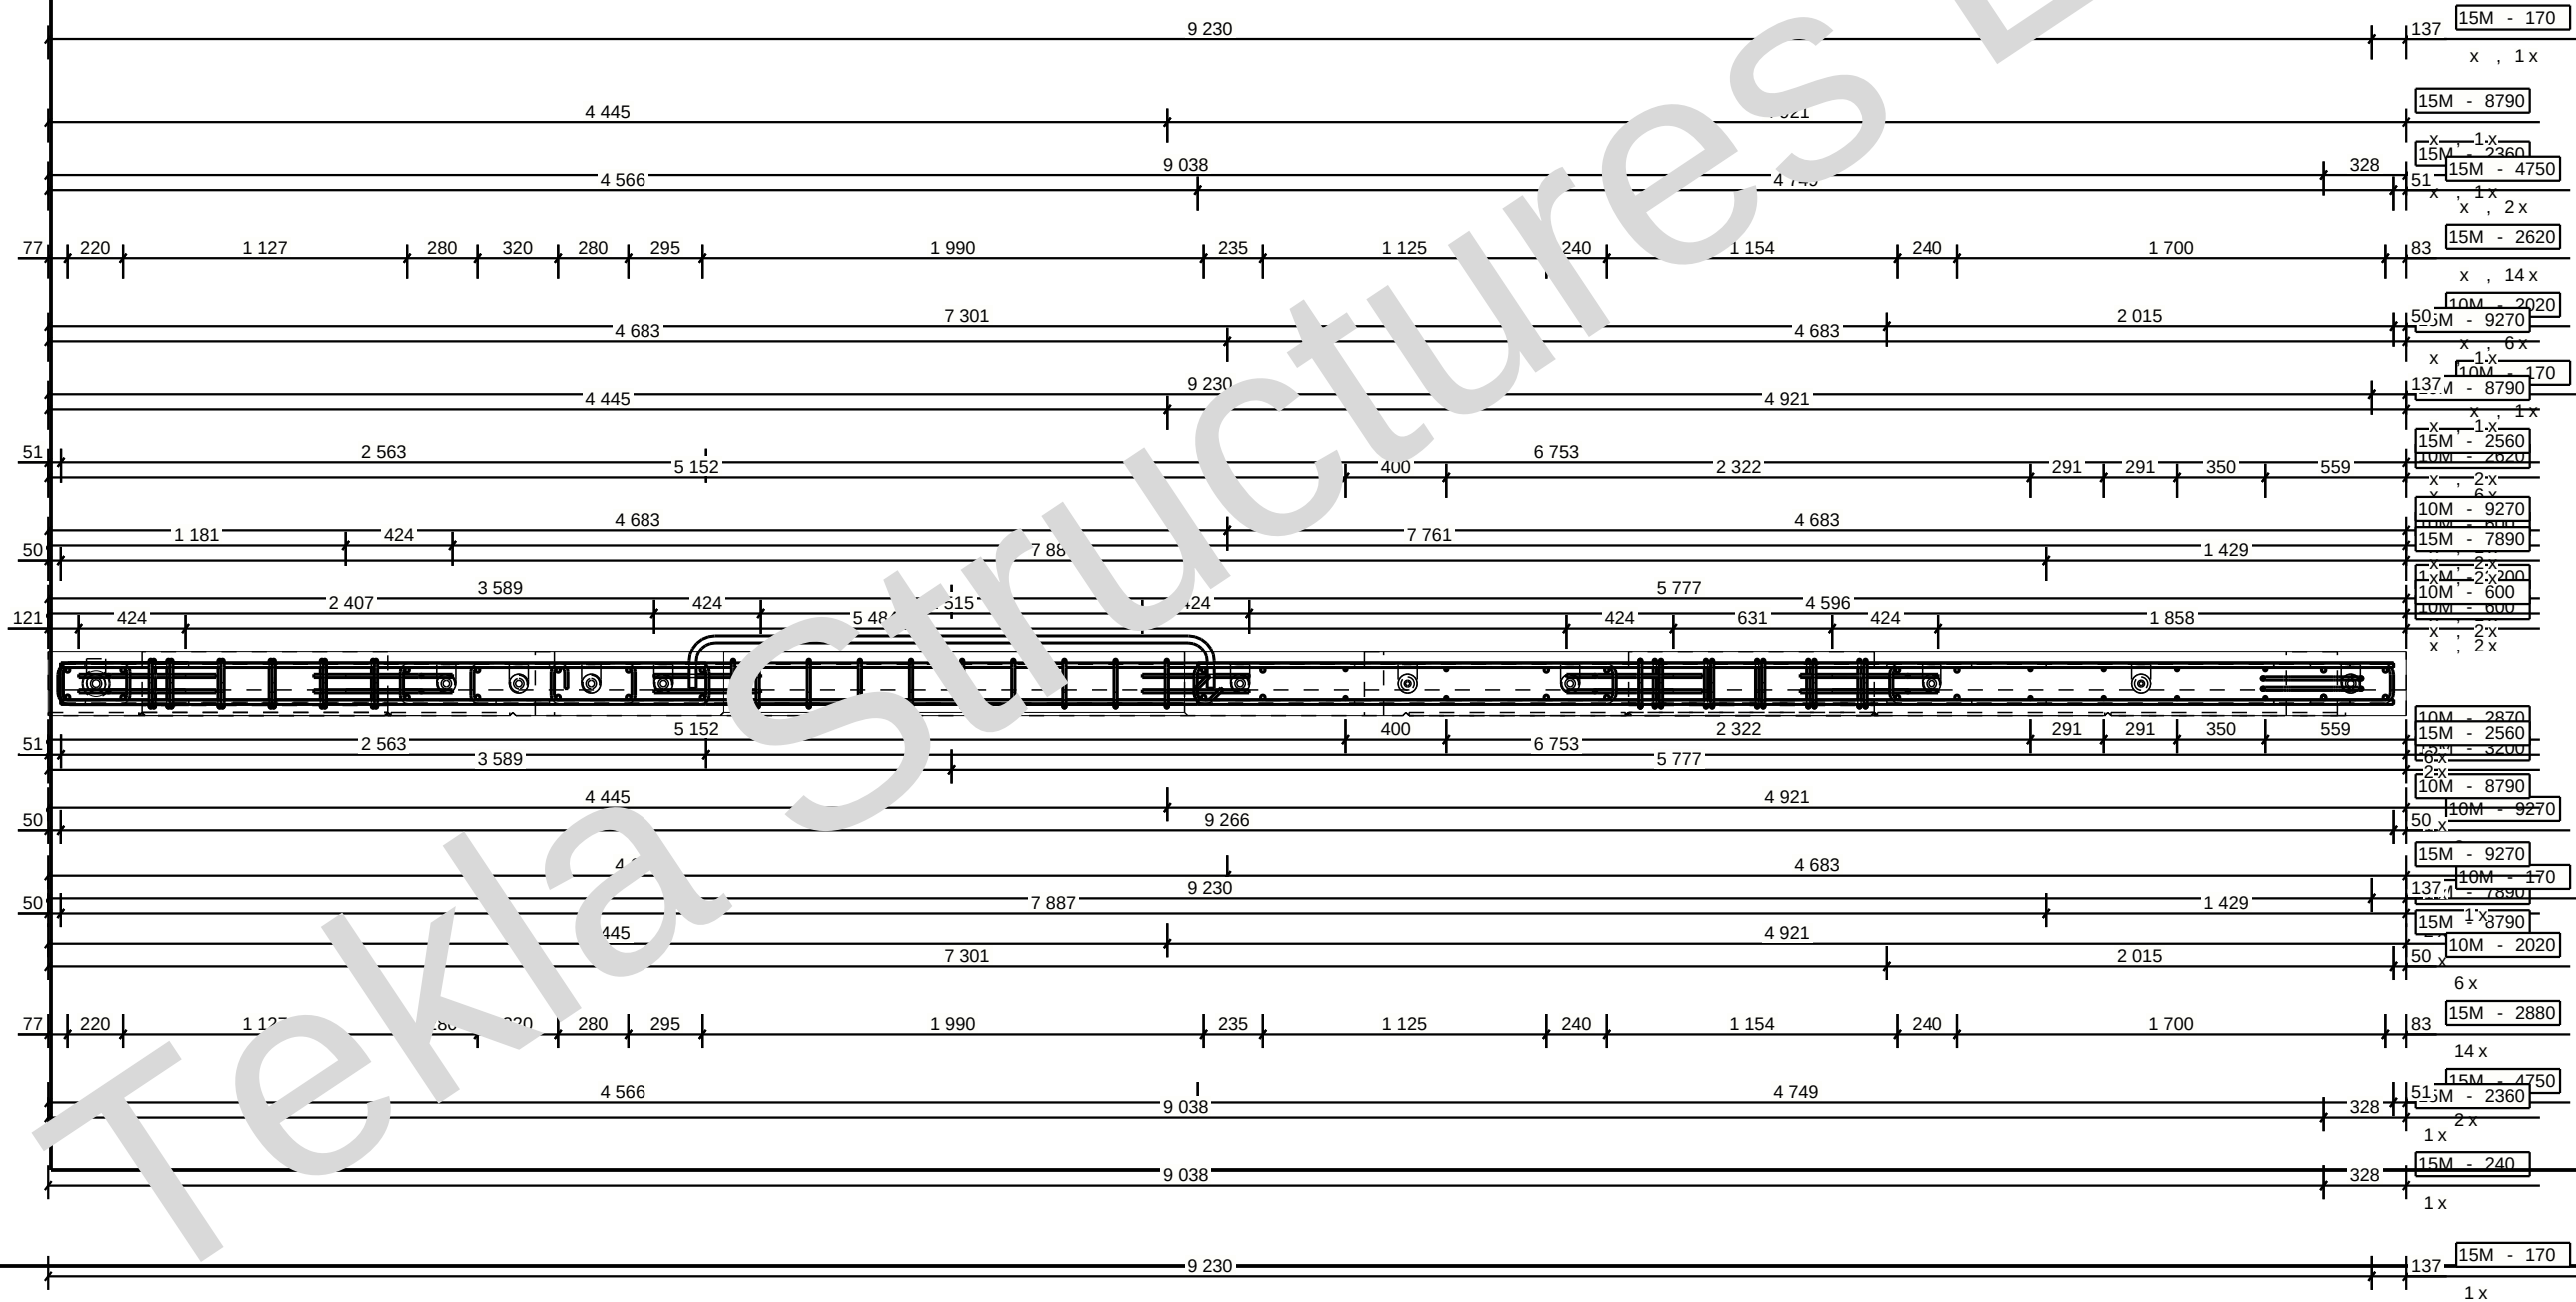

BILL OF MATERIALS			
MARK	QTY.	DESCRIPTION	LENGTH AREA
RB10M 00	1	10M - 17	3790
RB10M 06	19	10M - 17	760
10M 0	12	10M - T1	890
RE 10050	12	10M - Unknown	4240
RB10M 051	8	10M - TS5_1	750
RB10M 052	13	10M - TS67_2	1090
10M 0125	4	10M - 14	860
RB10M 0135	22	10M - Unknown	16910
F552	2	15M - Unknown	114
RB25M 0139	1	15M - 17	2380
	2	10M - STR	170
	12	10M - STR	600
	12	10M - STR	2020
	6	10M - STR	2620
	6	10M - STR	2870
	2	10M - STR	8790
	3	10M - STR	9270
	14	15M - STR	2880
	2	15M - STR	3200
	4	15M - STR	4750
	4	15M - STR	7890
	2	15M - STR	8790
	2	15M - STR	9270

STUBBE'S PRECAST			
PROJECT: PAISLEY TOWER			
PROJECT CODE: PTR	PAINT CODE:	UNITS REQD.: 1	
DRAWN BY:	DATE: 02.10.2026	SCALE: AS SHOWN	
ENGINEER:	DATE:	FILE:	
PROJECT No: P22-132		PIECE MARK: PAGE - 3	

REINFORCING BILL OF MATERIALS																			
REINF. MARK	QTY	SIZE	GRADE	BND TYP	LENGTH/ AREA	A	B	C	D	E	F	G	H	H2	J	K	K2	O	PIN DIA.
RB10M 0040	10	10M	400W	T1	3790	75	160	1675	160	1675		75							60
RB10M 0046	19	10M	400W	17	760		330	160	330										60
RB10M 0049	12	10M	400W	T1	890	85	190	195	190	195		85							40
RB10M 0050	12	10M	400W	Un***	4240														
RB10M 0051	8	10M	400W	TS5_1	750	255	255	255											60
RB10M 0052	13	10M	400W	TS***	1090	100	160	280	160	280	160	100							40
RB10M 0125	4	10M	400W	14	860	200	140	210	140	200			100	100				405	60
RB10M 0135	22	10M	400W	Un***	1690														
RB15M 0068	2	15M	400W	Un***	1140														
RB25M 0139	1	25M	400W	17	2380		210	2085	210										150
	2	10M	400W	STR	170		170												
	12	10M	400W	STR	600		600												
	12	10M	400W	STR	2020		2020												
	6	10M	400W	STR	2620		2620												
	6	10M	400W	STR	2870		2870												
	2	10M	400W	STR	8790		8790												
	3	10M	400W	STR	9270		9270												
	2	15M	400W	STR	170		170												
	1	15M	400W	STR	240		240												
	2	15M	400W	STR	2360		2360												
	4	15M	400W	STR	2560		2560												
	14	15M	400W	STR	2620		2620												
	14	15M	400W	STR	2880		2880												
	2	15M	400W	STR	3200		3200												
	4	15M	400W	STR	4750		4750												
	4	15M	400W	STR	7890		7890												
	2	15M	400W	STR	8790		8790												
	2	15M	400W	STR	9270		9270												

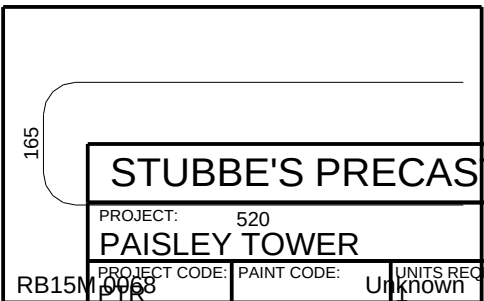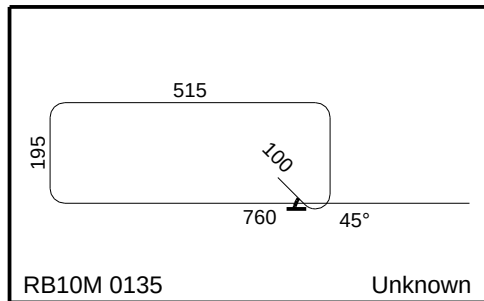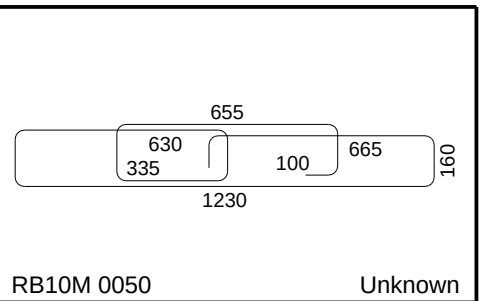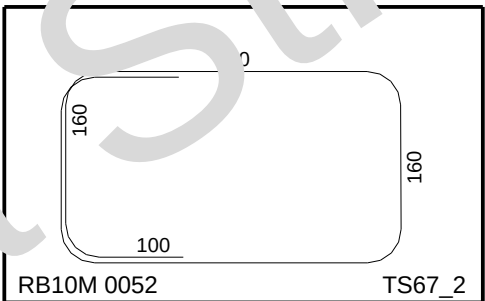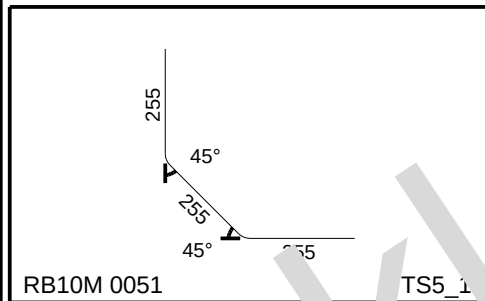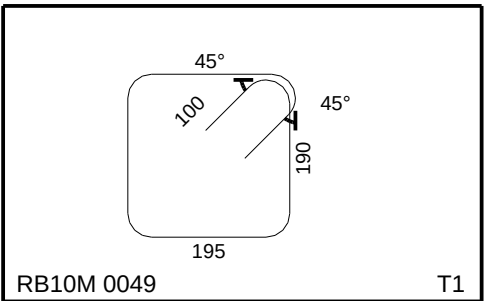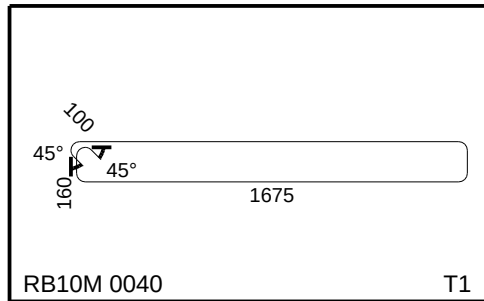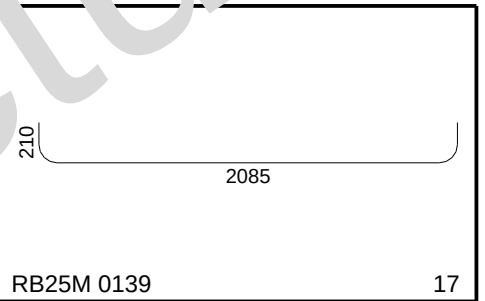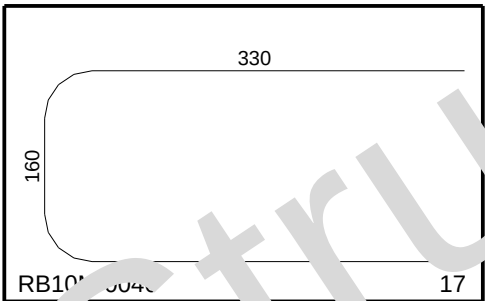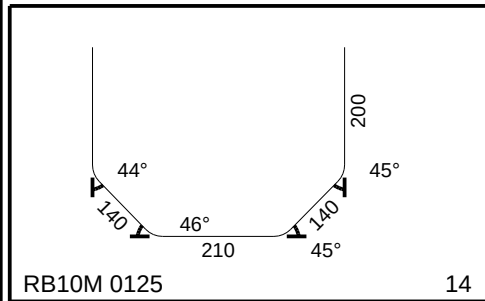

STUBBE'S PRECAST

PROJECT: 520	
PAISLEY TOWER	
PROJECT CODE: PPR	PAINT CODE: Unknown
DRAWN BY:	DATE: 02.10.2026
ENGINEER: NA	DATE:
PROJECT No: P22-132	PIECE MARK: