




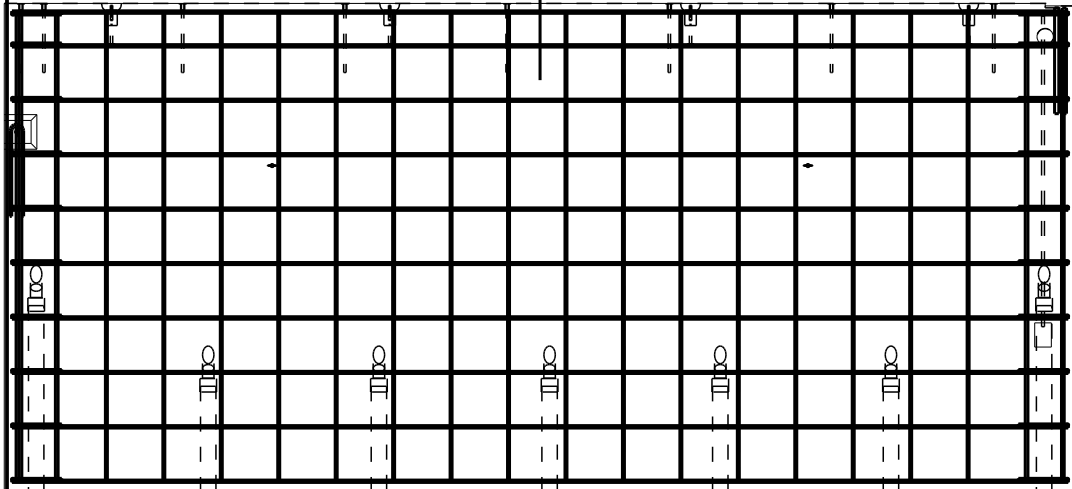

TOP IN FORM
1:50

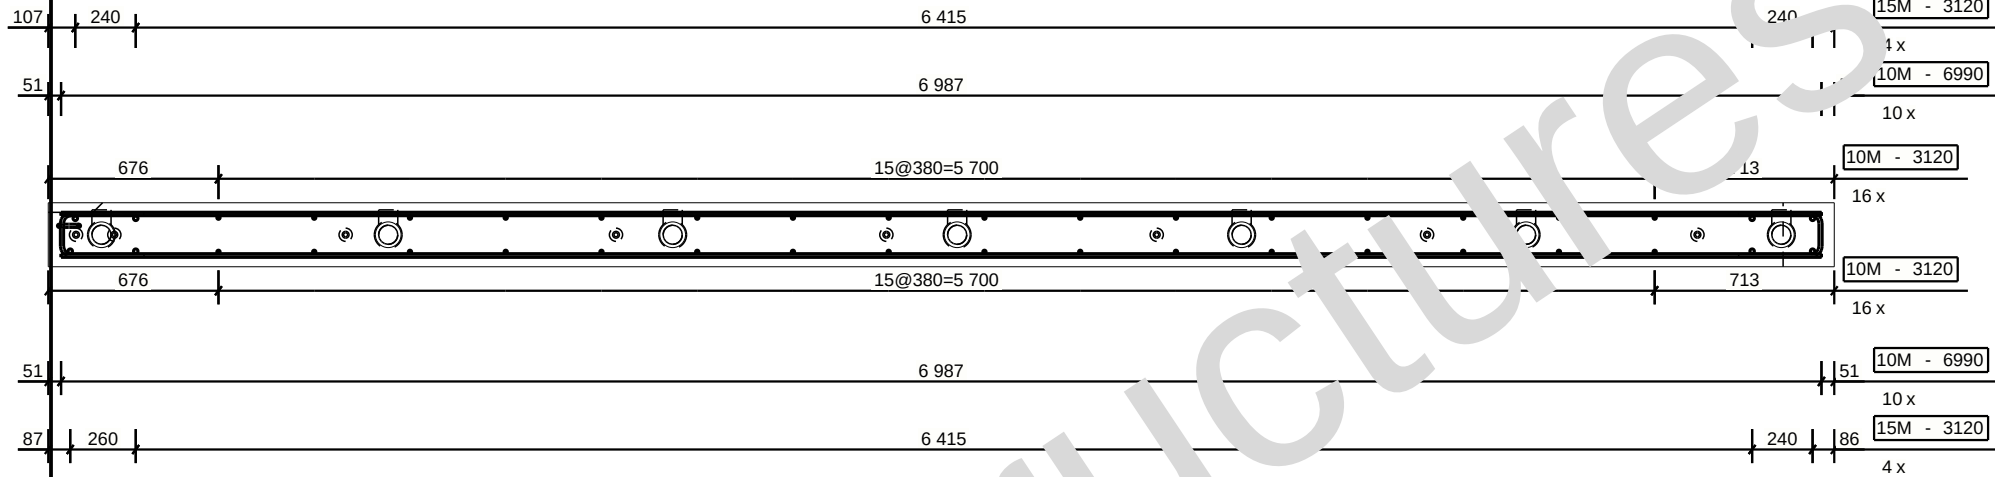

VIEW END
1:30

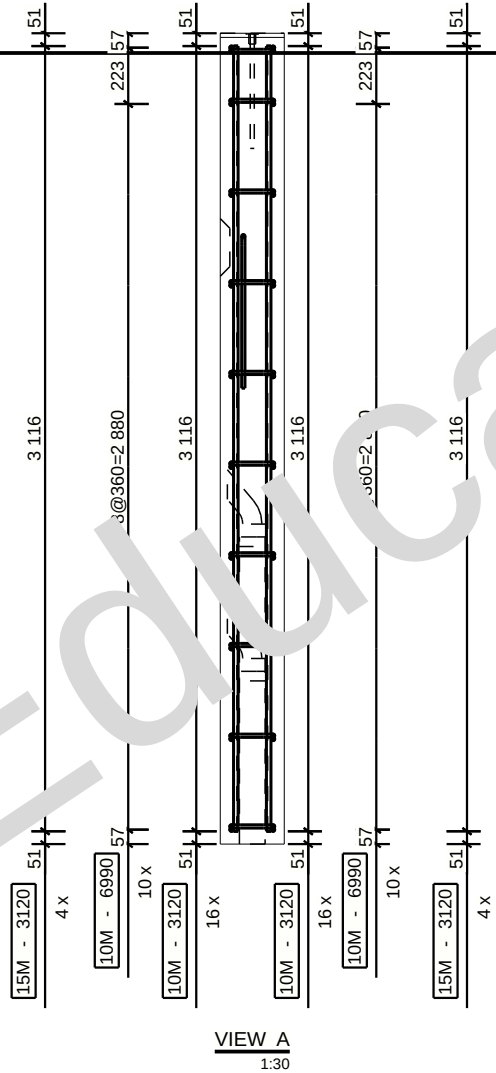

VIEW A
1:30

MIN. COVER				2 mm
BILL OF MATERIALS				
MARK	QTY.	DESCRIPTION	LENGTH	AREA
RB10M 00	1	10M - 1	1250	
RB10M 04	20	10M - 17	780	
	32	10M - STR	3120	
	40	10M - STR	6990	
	8	15M - STR	3120	

STUBBE'S PRECAST		
PROJECT:		
PAISLEY TOWER		
PROJECT CODE:	PAINT CODE:	UNITS REQD.:
PTR		1
DRAWN BY:	DATE:	SCALE:
	22.09.2026	AS SHOWN
ENGINEER:	DATE:	FILE:
PROJECT No:	PIECE MARK:	
P22-132	W10-43	
	PAGE - 2	