


REINF. MARK	QTY	SIZE	GRADE	BND TYP	LENGTH/ AREA	A	B
RB10M 0001	1	10M	400W	S11	1250		1270
RB10M 0014	20	10M	400W	17	780		330
	32	10M	400W	STR	3120		3120
	48	10M	400W	STR	6936		6936
	8	15M	400W	STR	3120		3120

REINFORCING BILL OF MATERIALS

C	D	E	F	G	H	H2	J	K	K2	O	PIN DIA.
					610					90	5
180	330										60

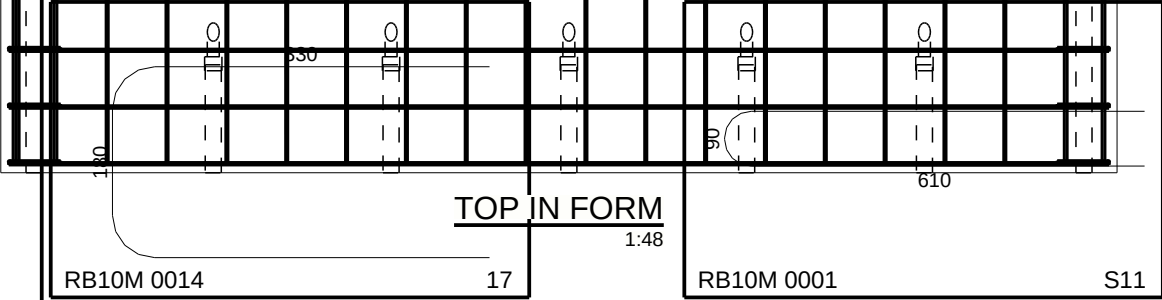

STUBBE'S PRECAST		
PROJECT: PAISLEY TOWER		
PROJECT CODE: PTR	PAINT CODE:	UNITS REQD.: 1
DRAWN BY:	DATE: 22.09.2026	SCALE: AS SHOWN
ENGINEER: NA	DATE:	FILE:
PROJECT No: P22-132	PIECE MARK: W10-43 PAGE - 3	