



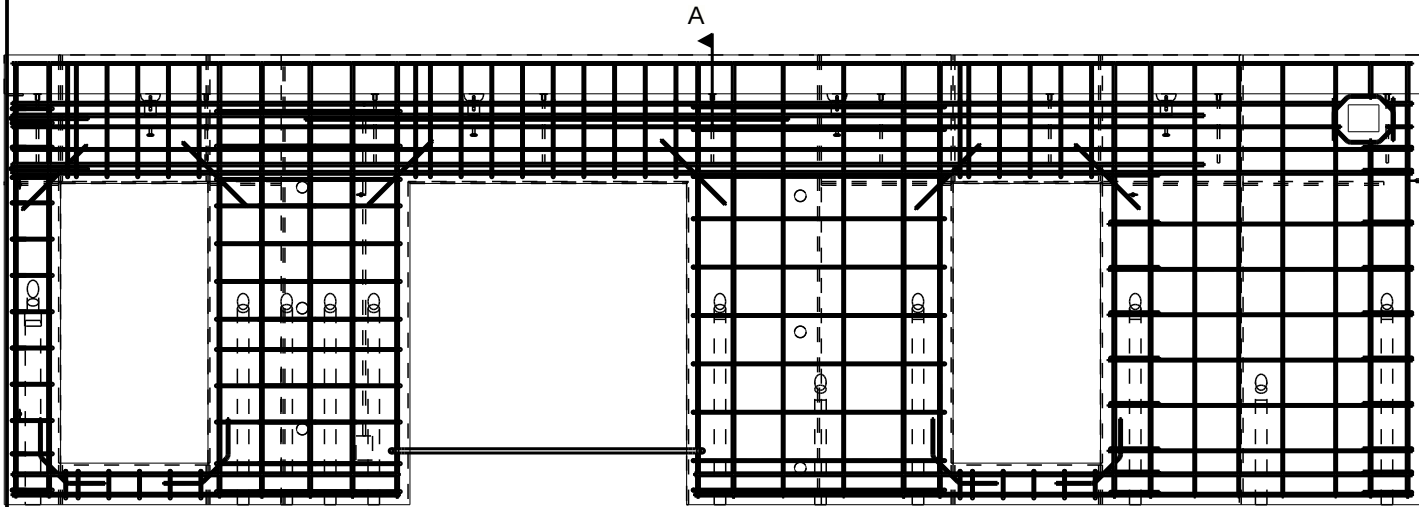

TOP IN FORM
1:50

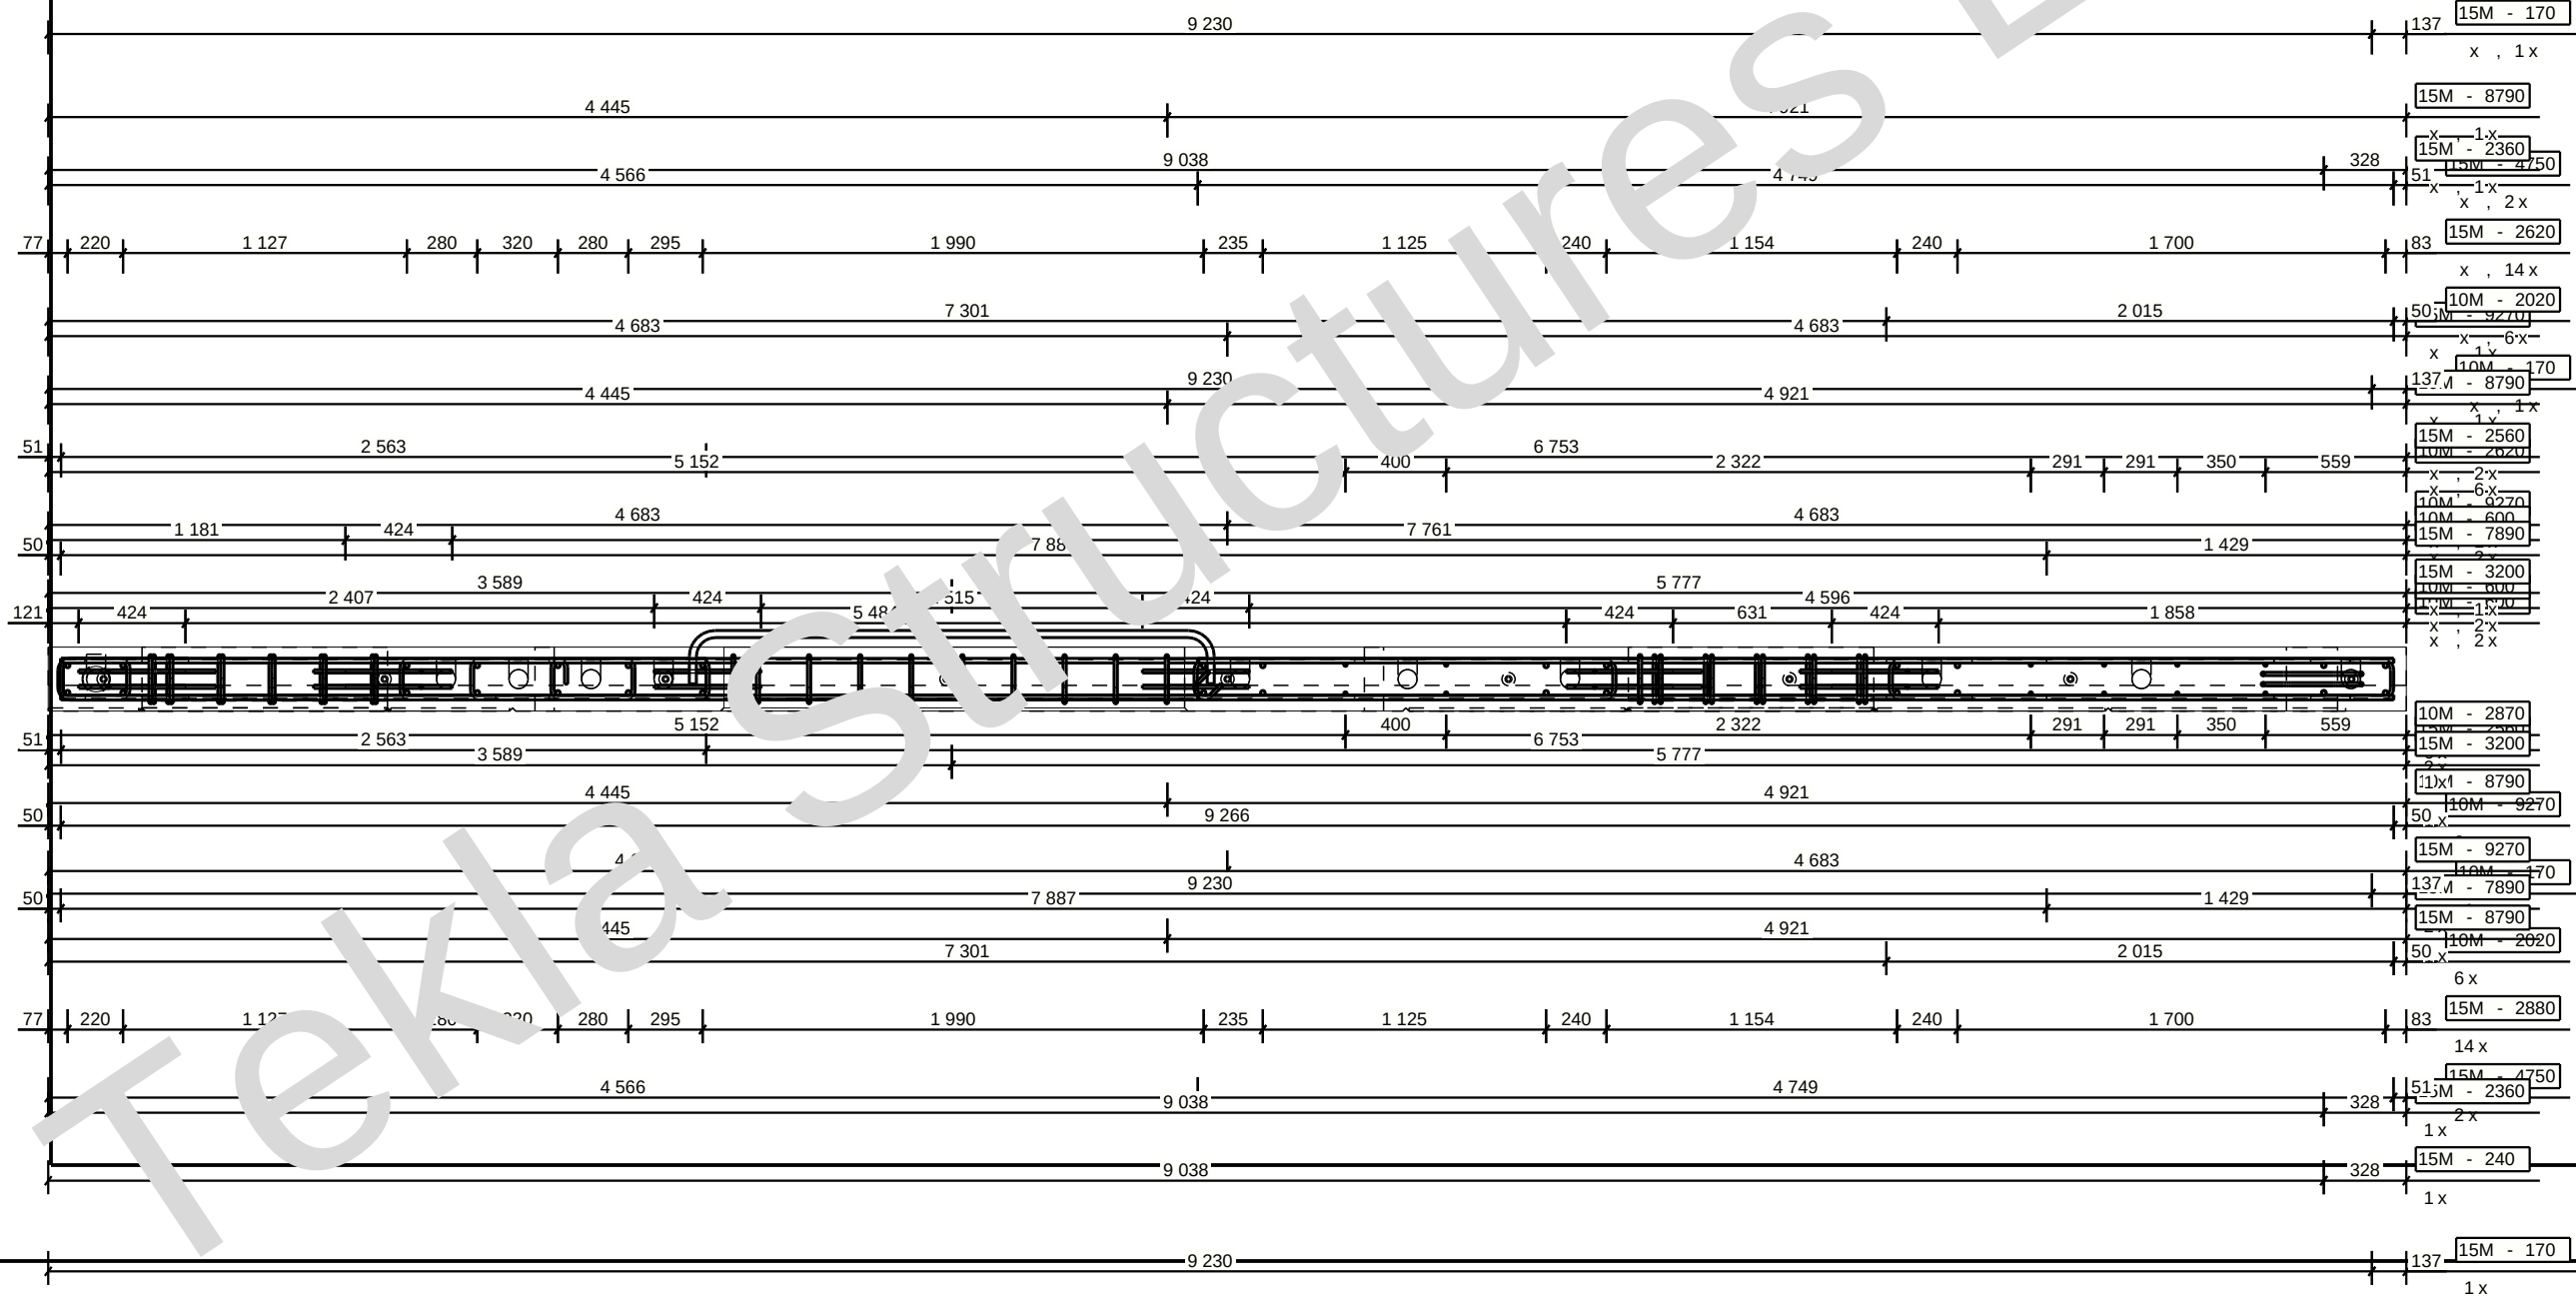

VIEW END 2
1:30

MARK	QTY.	DESCRIPTION	LENGTH	AREA
RB10M 000	1	10M - 170	3790	
RB10M 006	19	10M - 170	760	
RB10M 007	12	10M - T1	890	
RB10M 005	12	10M - Unknown	4240	
RB10M 0051	8	10M - TS5_1	750	
RB10M 0052	13	10M - TS67_2	1090	
RB10M 0125	4	10M - 14	860	
RB10M 0135	22	10M - Unknown	16910	
FB55M 0068	2	15M - Unknown	114	
RB25M 0139	1	15M - 17	2380	
	2	10M - STR	170	
	12	10M - STR	600	
	12	10M - STR	2020	
	6	10M - STR	2620	
	6	10M - STR	2870	
	2	10M - STR	8790	
	3	10M - STR	9270	
	14	15M - STR	2880	
	2	15M - STR	3200	
	4	15M - STR	4750	
	4	15M - STR	7890	
	2	15M - STR	8790	
	2	15M - STR	9270	

VIEW A
1:30

STUBBE'S PRECAST		
PROJECT: PAISLEY TOWER		
PROJECT CODE: PTR	PAINT CODE:	UNITS REQD.: 1
DRAWN BY:	DATE: 22.09.2026	SCALE: AS SHOWN
ENGINEER:	DATE:	FILE:
PROJECT No: P22-132		PIECE MARK: W10-50 PAGE - 2