



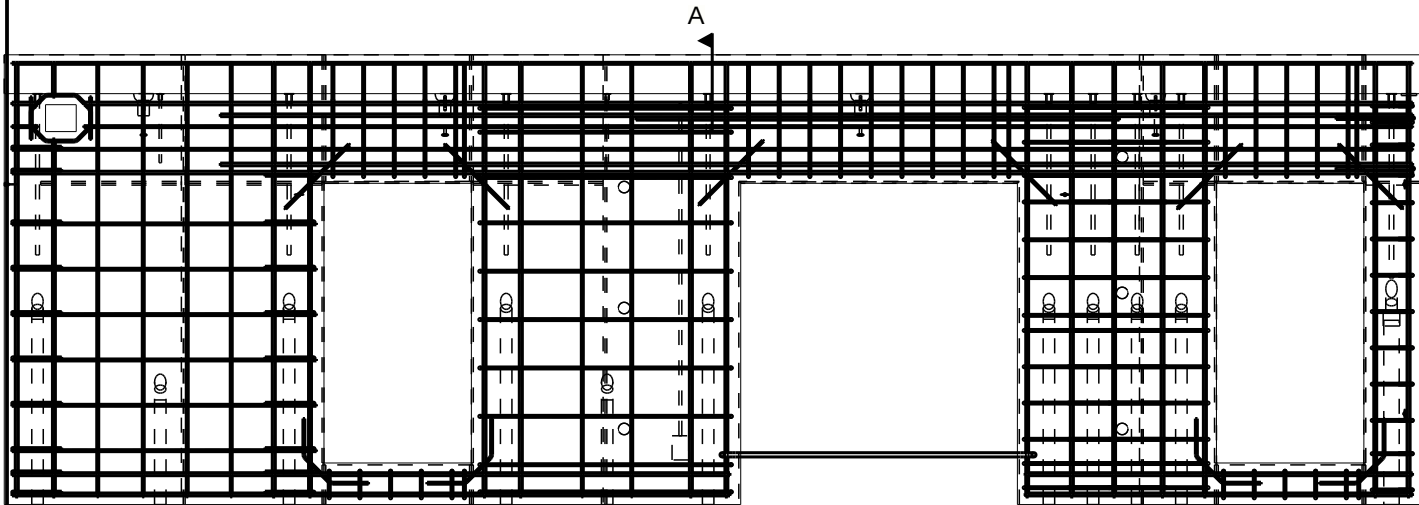

TOP IN FORM
1:50

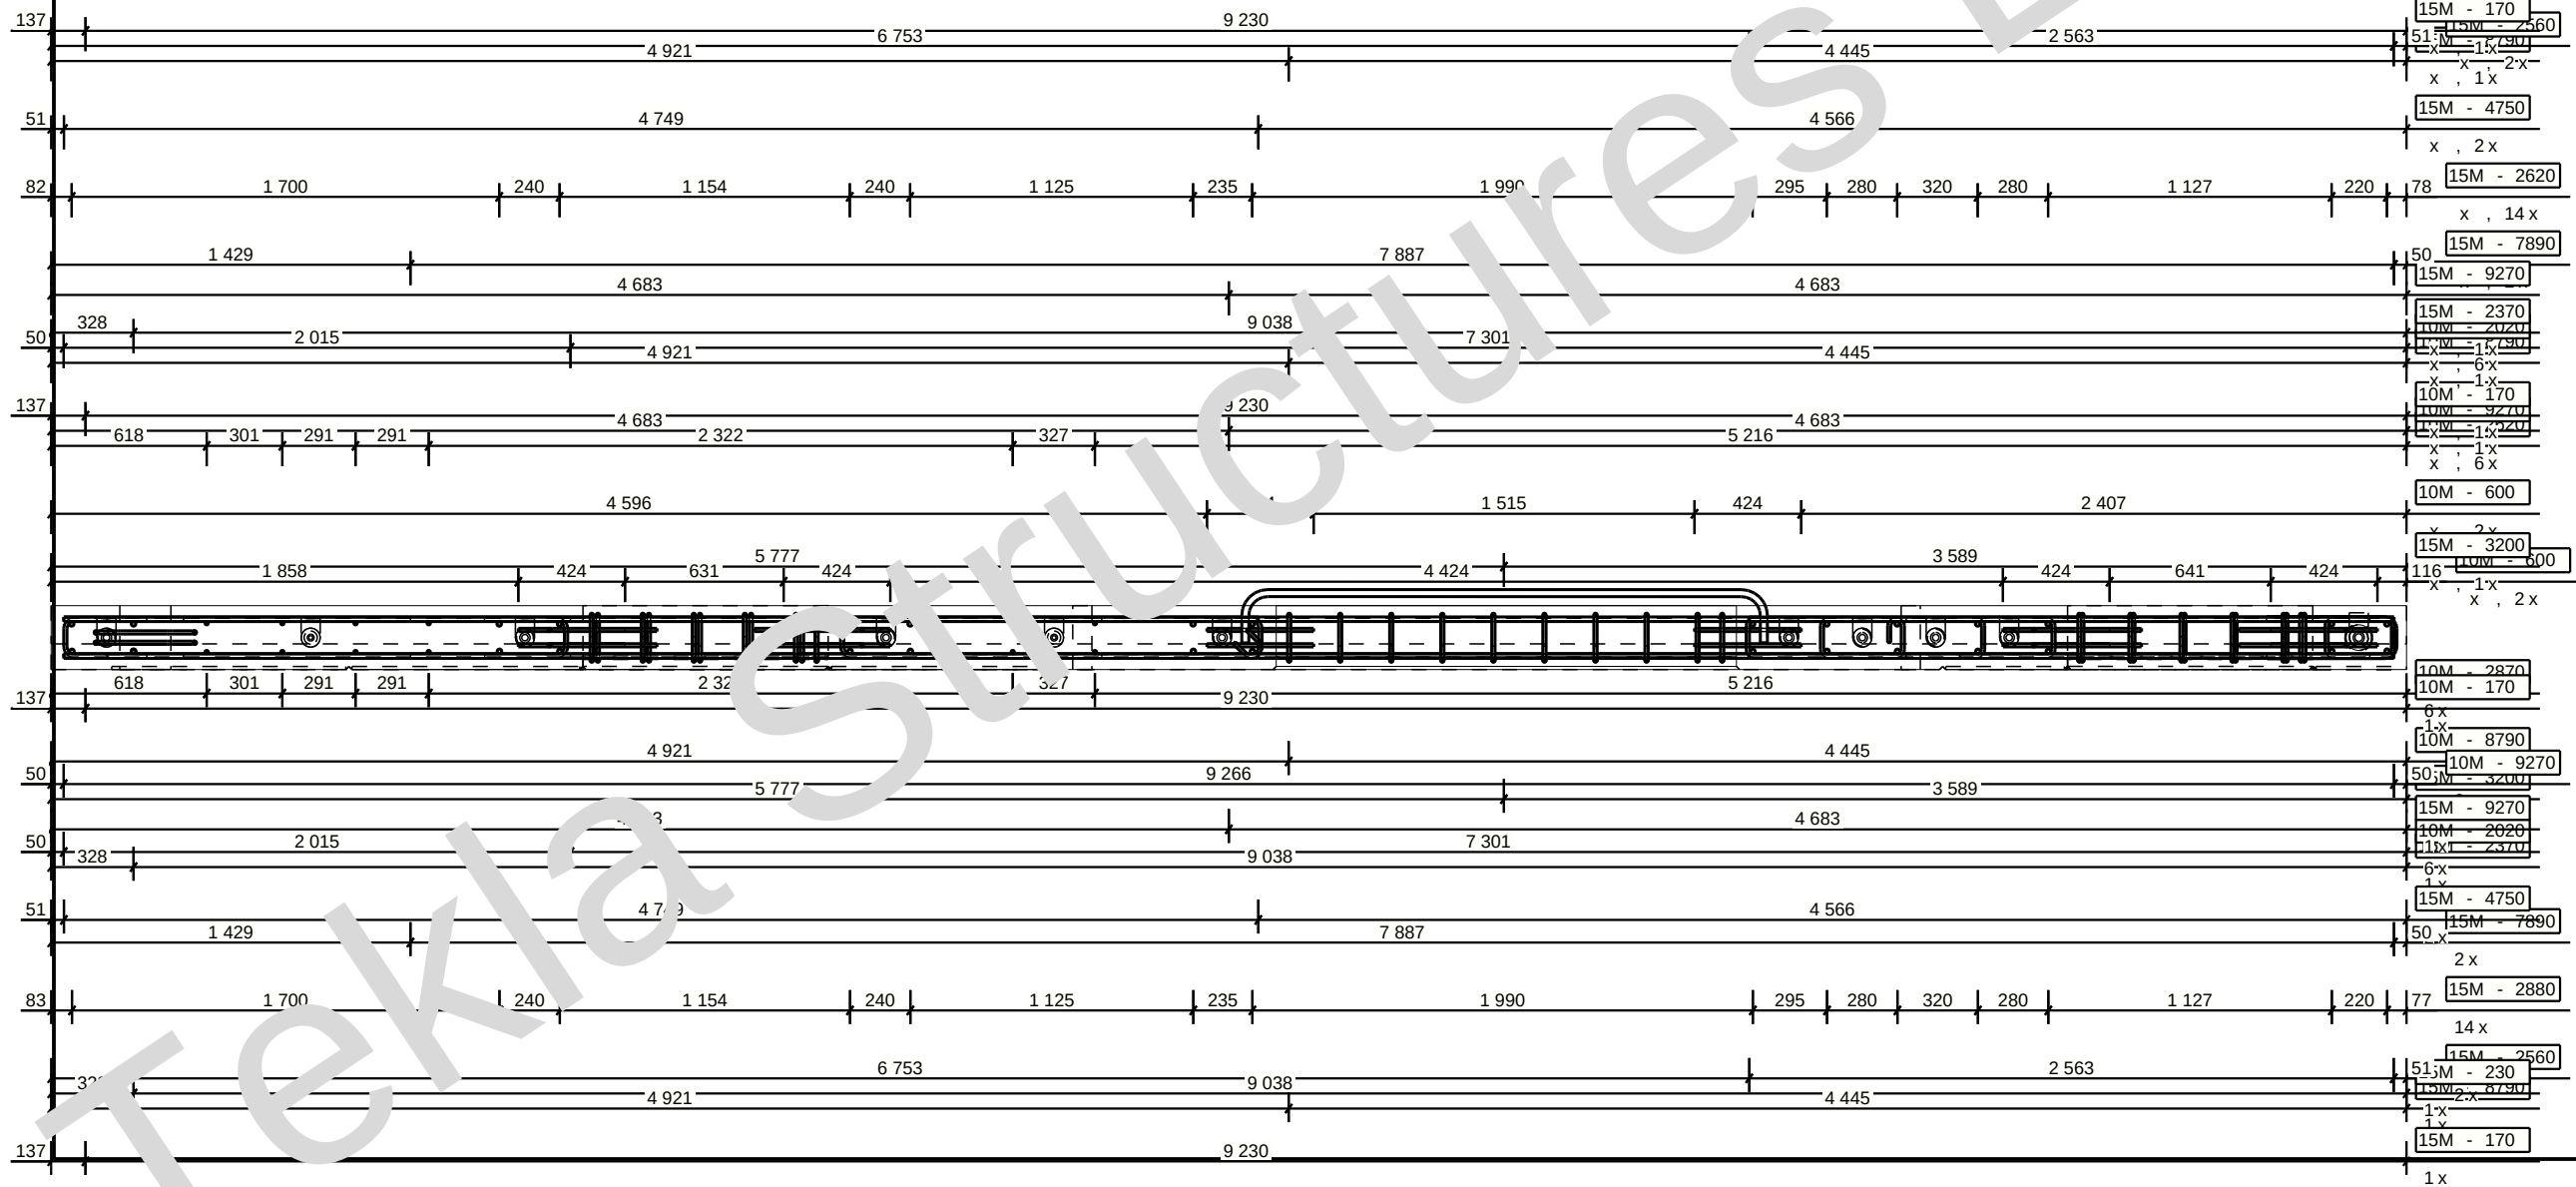

VIEW END 2
1:30

MARK	QTY.	DESCRIPTION	LENGTH	AREA
RB10M 0001	10	10M - T1	860	3790
RB10M 0002	19	10M - T1	760	890
RB10M 0003	13	10M - T1	4240	750
RB10M 0004	8	10M - TS5_1	1090	169.6
RB10M 0005	22	10M - Unknown	114.2	2380
RB10M 0006	2	10M - STR	170	600
RB10M 0007	12	10M - STR	2020	2620
RB10M 0008	6	10M - STR	2870	8790
RB10M 0009	2	10M - STR	9270	170
RB10M 0010	14	15M - STR	2880	4750
RB10M 0011	4	15M - STR	7890	8790
RB10M 0012	2	15M - STR	9270	3200
RB10M 0013	2	15M - STR	2370	2020
RB10M 0014	2	15M - STR	2370	2370

STUBBE'S PRECAST

PROJECT: PAISLEY TOWER		
PROJECT CODE: PTR	PAINT CODE:	UNITS REQD.: 1
DRAWN BY:	DATE: 22.09.2026	SCALE: AS SHOWN
ENGINEER:	DATE:	FILE:
PROJECT No: P22-132		PIECE MARK: W10-59
		PAGE - 2