


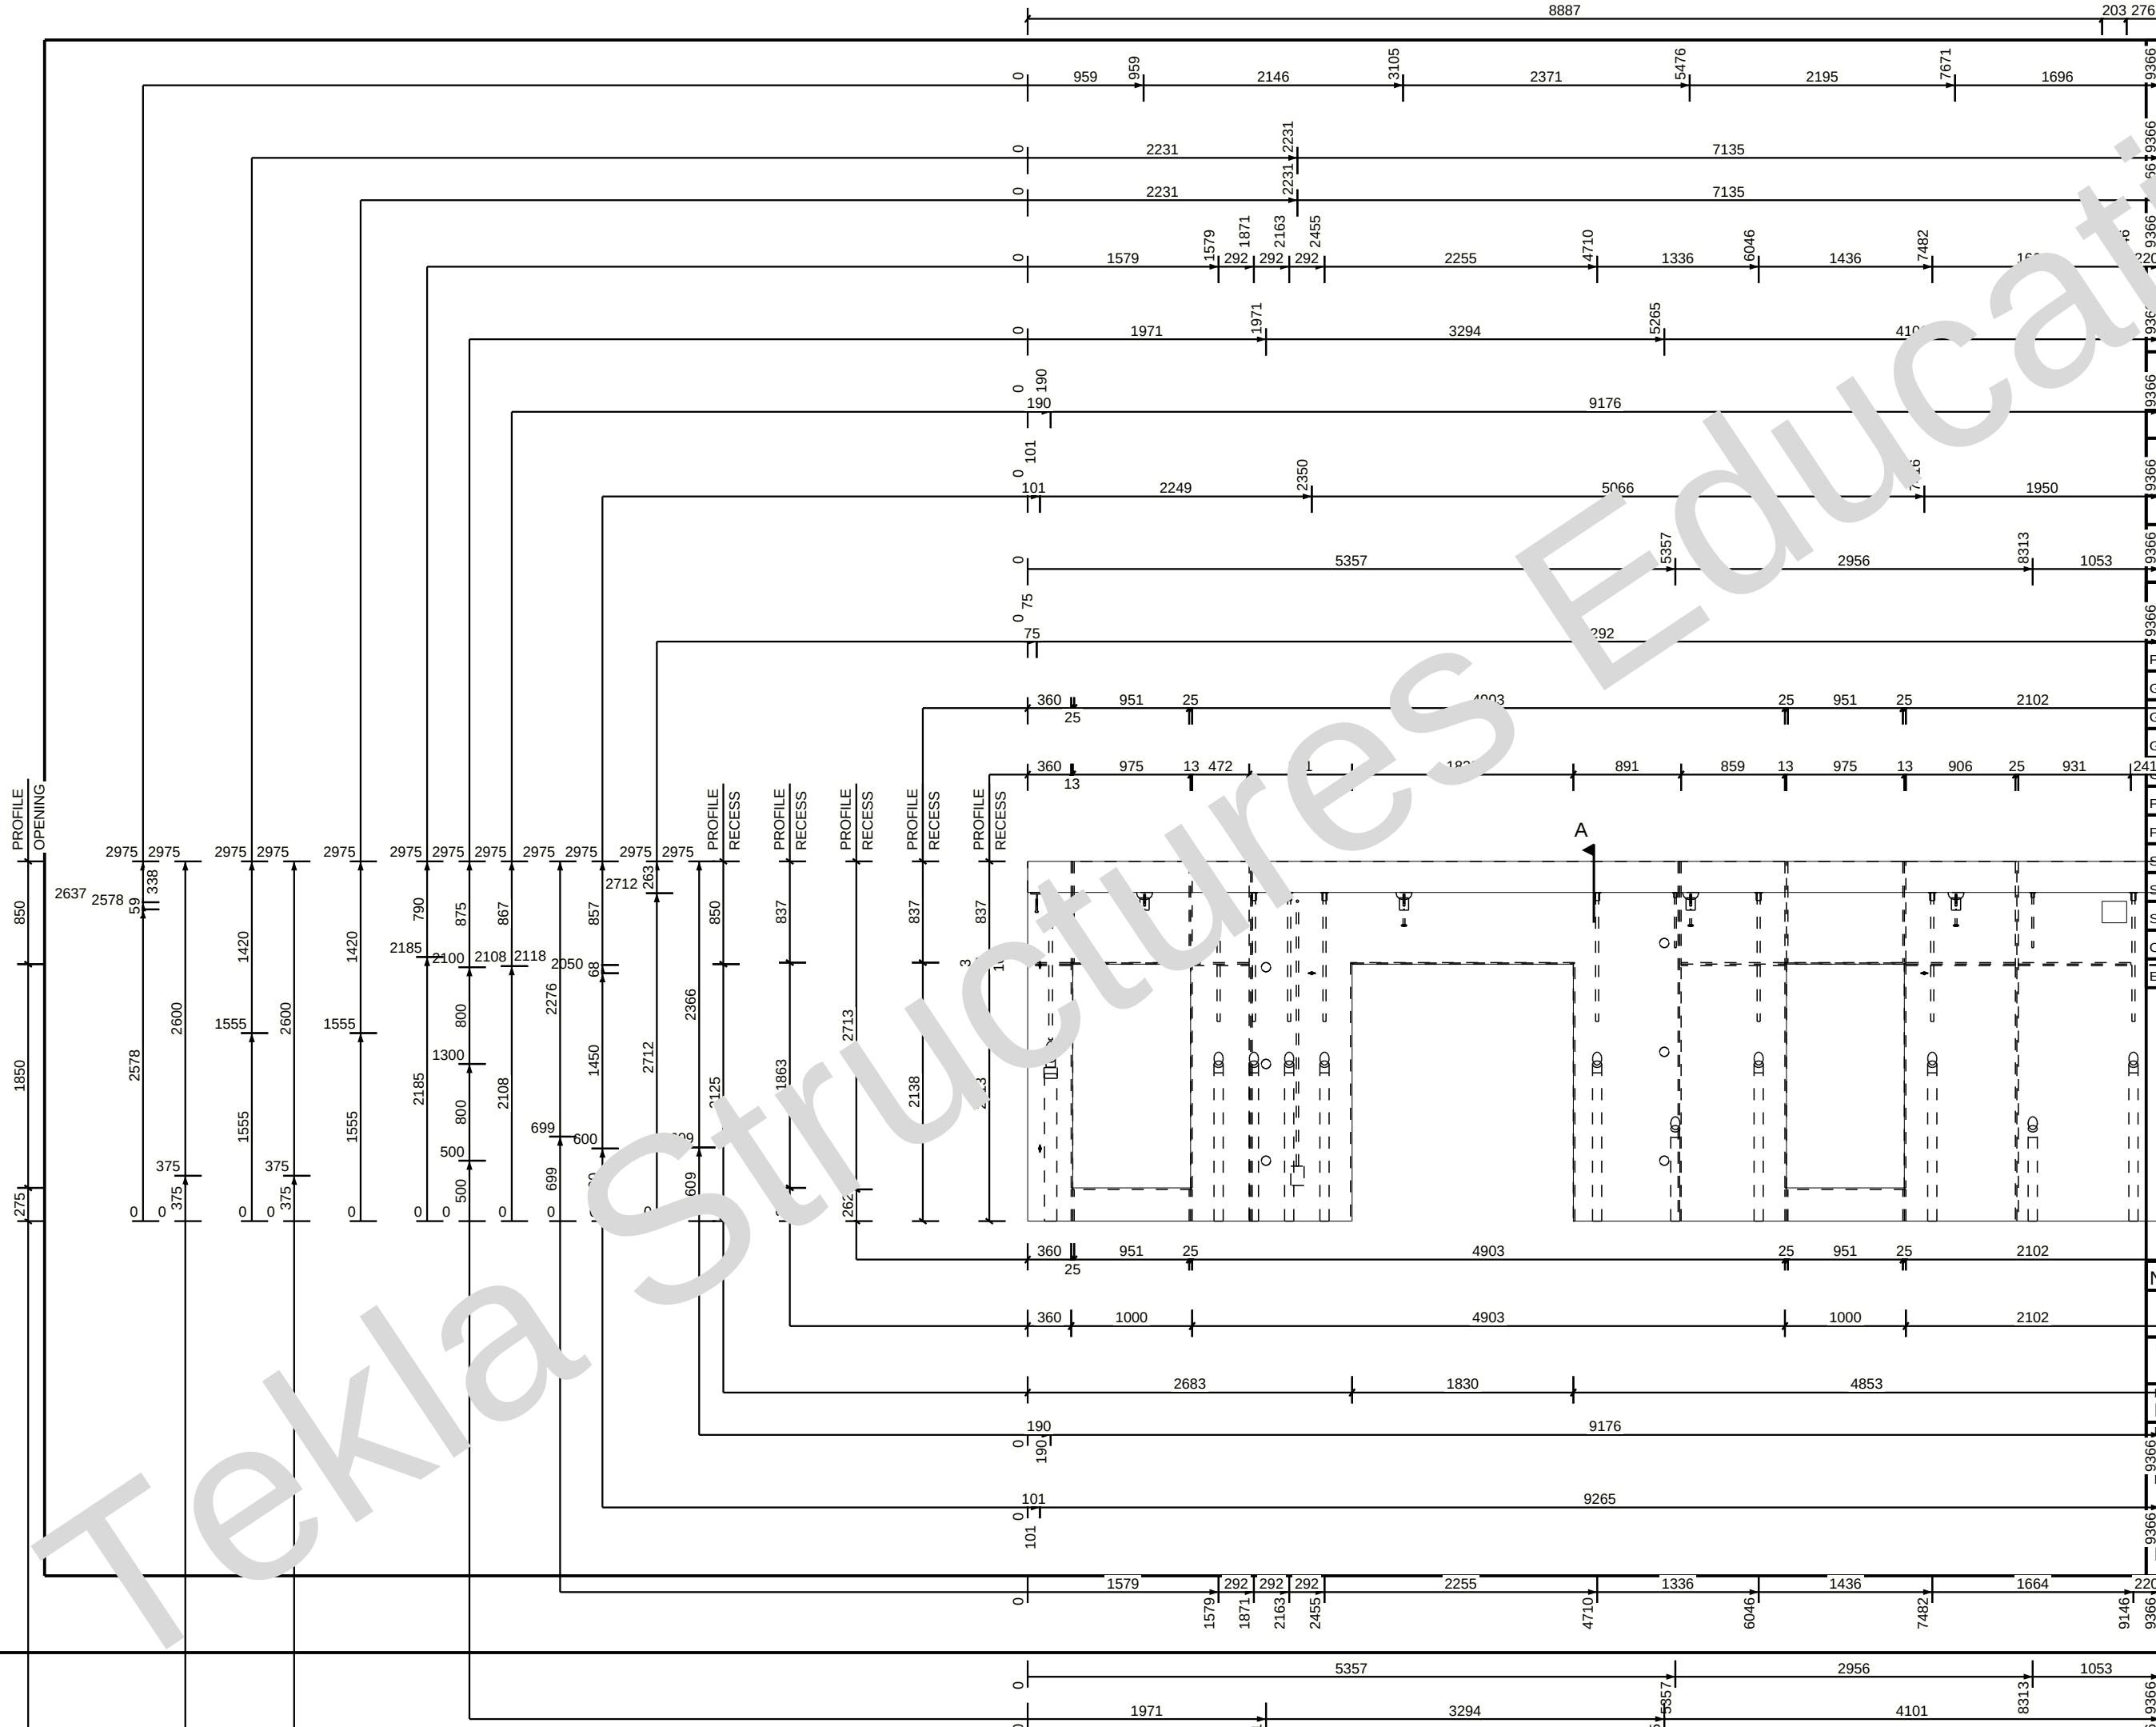

GENERAL NOTES		
1) 28 DAY (MPa)	0	
2) STRIPPING (M)	0	
3) WEIGHT (KGS)	24822	
4) AIR CONTENT (%)	4% TO 7%	
5) MIN. COVER	25 mm	
6) CLAS	F2	
7) CONC. VOLUME (yd³)	6.05	
FINISH/NOTES		
1) FLOOR FINISH	SCREED	
2) WALL SIDE		
3) GT75-254		
4) END 1		
5) HARDWARE		
6) END 2		
7) SP30-1219		
8) HARDWARE		
9) P-300		
10) HARDWARE		
11) SP15-457		
12) HARDWARE		
BILL OF MATERIALS		
ITEM No.	DESCRIPTION	QTY.
P-602	2000LB FORGED ANCHOR	4
GT75-686	75Ø x 686 GROUT TUBE	2
GT RECESS	75Ø x 1219 GROUT TUBE	8
GT76-254	76Øx254mm G.TUBE	6
GT RECESS	76Øx1219 GROUT TUBE	1
P-300	19MM WERT PROFILE RECESS	1
P-602	13 PROFILE RECESS	1
SP15-457	15MM 457 WILLIAMS SPL	1
SP25-1067	SP25MMx1067 WILLIAMS \$	1
SP30-1219	30MM 1219 WILLIAMS SPL	1
CNDT	19MM CONDUIT	1
EB-S-PL	Single Plastic Electr	1
RECESS		
NO.	DATE	DESCRIPTION
PAINLEY TOWER		
PROJECT CODE:	PAINT CODE:	UNITS REQD.: 1
DATE:	DATE:	SCALE: AS SHOWN
ENGINEER: P-300	DATE:	FILE:
PROJECT NO.	PIECE MARK: W10-71	
P22-132	PAGE - 1	
GT75-1219		
HARDWARE		
GT75-686		
HARDWARE		
GT76-254		
HARDWARE		