
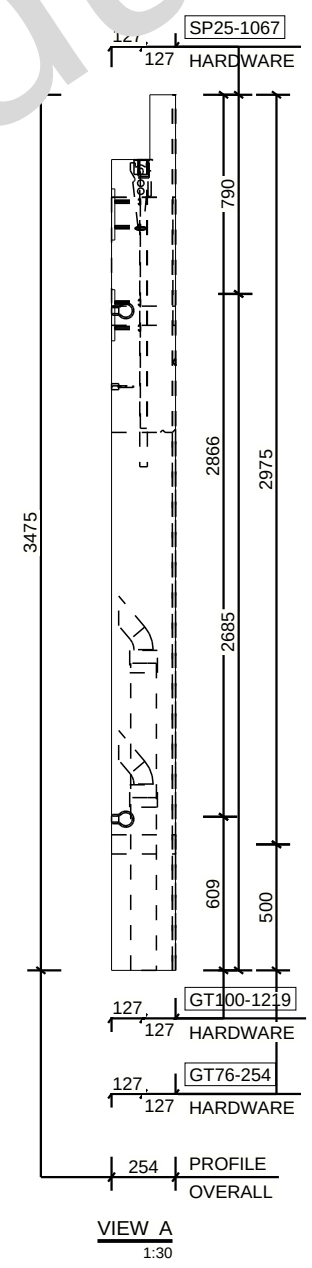


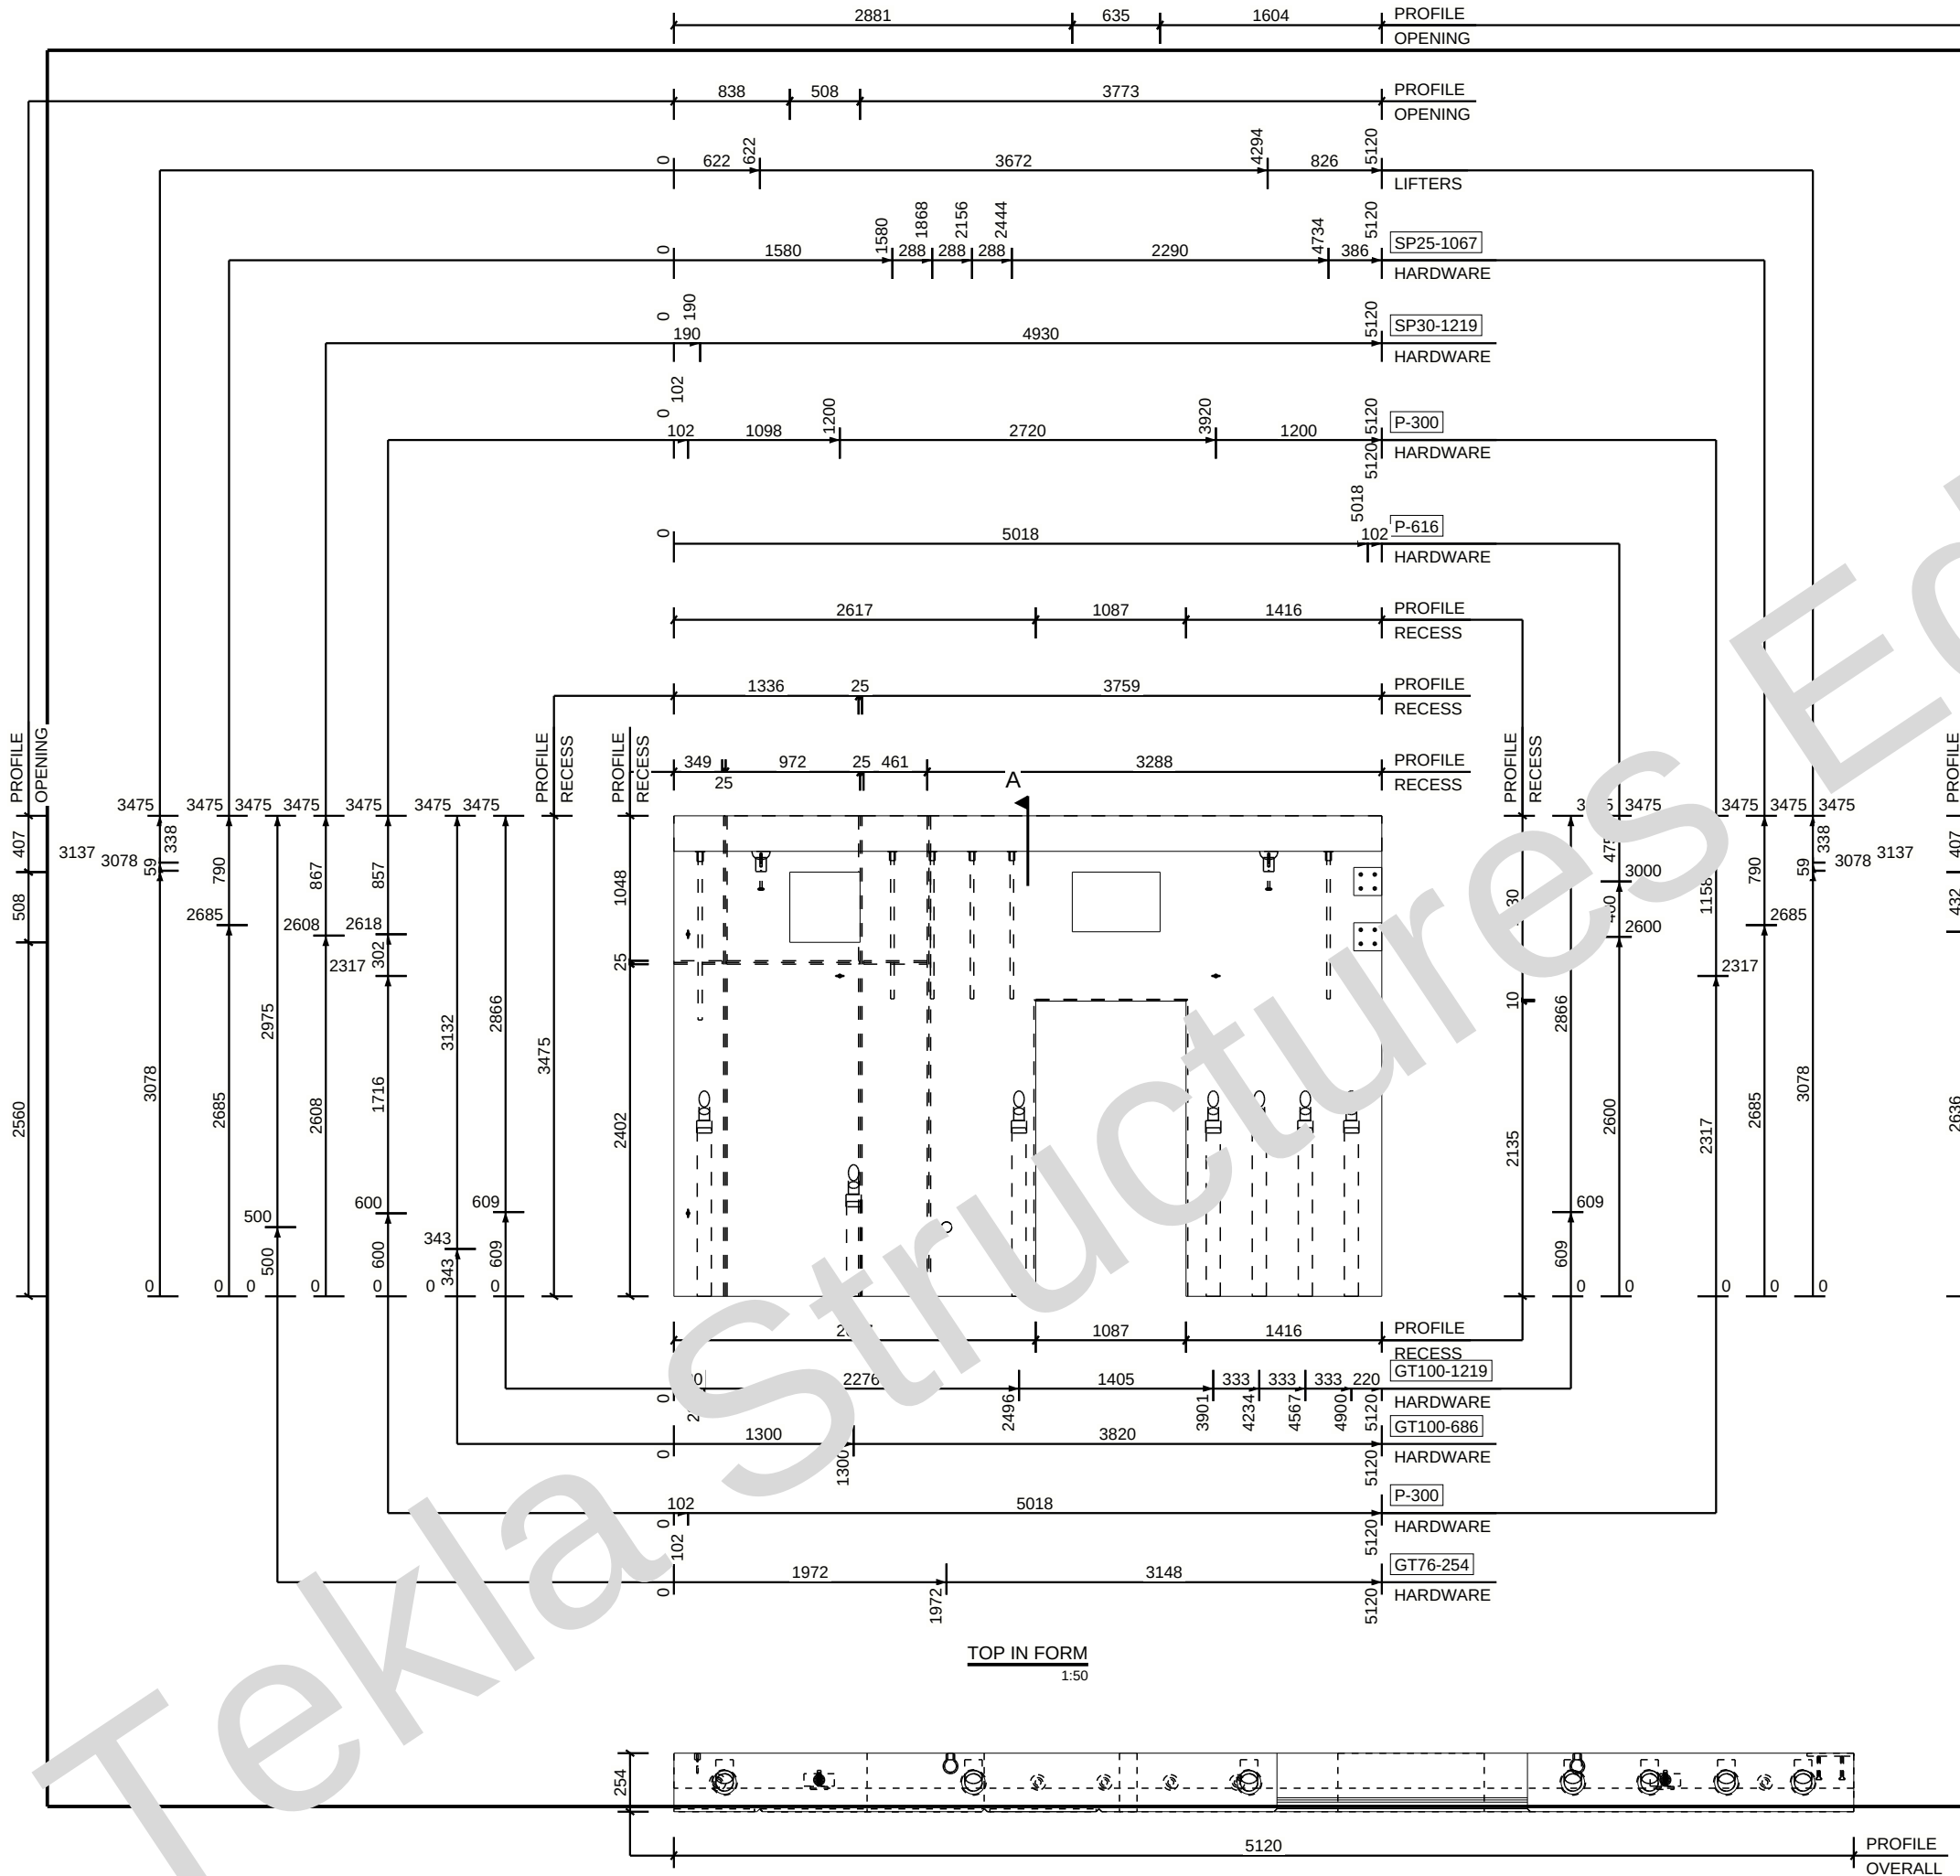

GENERAL NOTES				
1) 28 DAY (MPa)				0
2) STRIPPING (M)				0
3) WEIGHT (KGS)				18317
4) AIR ENTRAINED				4% TO 7%
5) MIN COVER				25 mm
6) CLASS				F2
7) CONCRETE VOLUME (yd³)				4.53
CHARACTER	B	T	E	FINISH/NOTES
TROWEL SIDE				SCREED
FORM SIDE				
END 1				
END 2				
SIDE A				
SIDE B				