




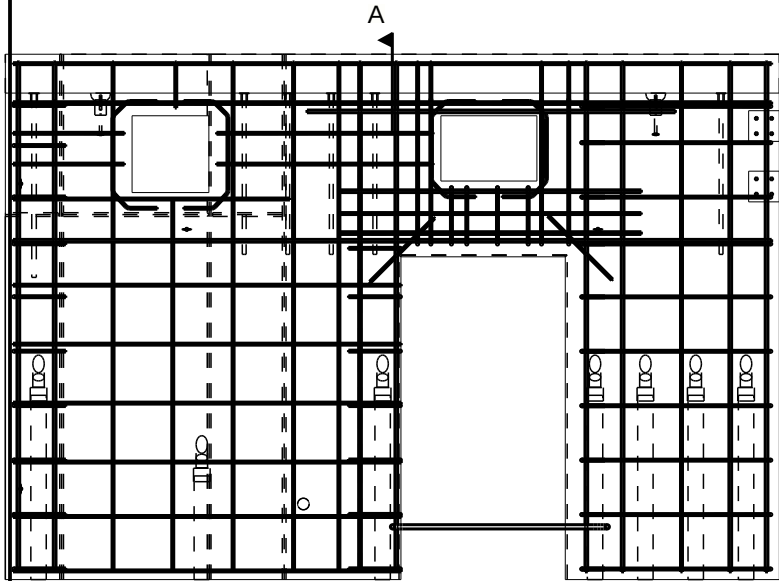

TOP IN FORM
1:50

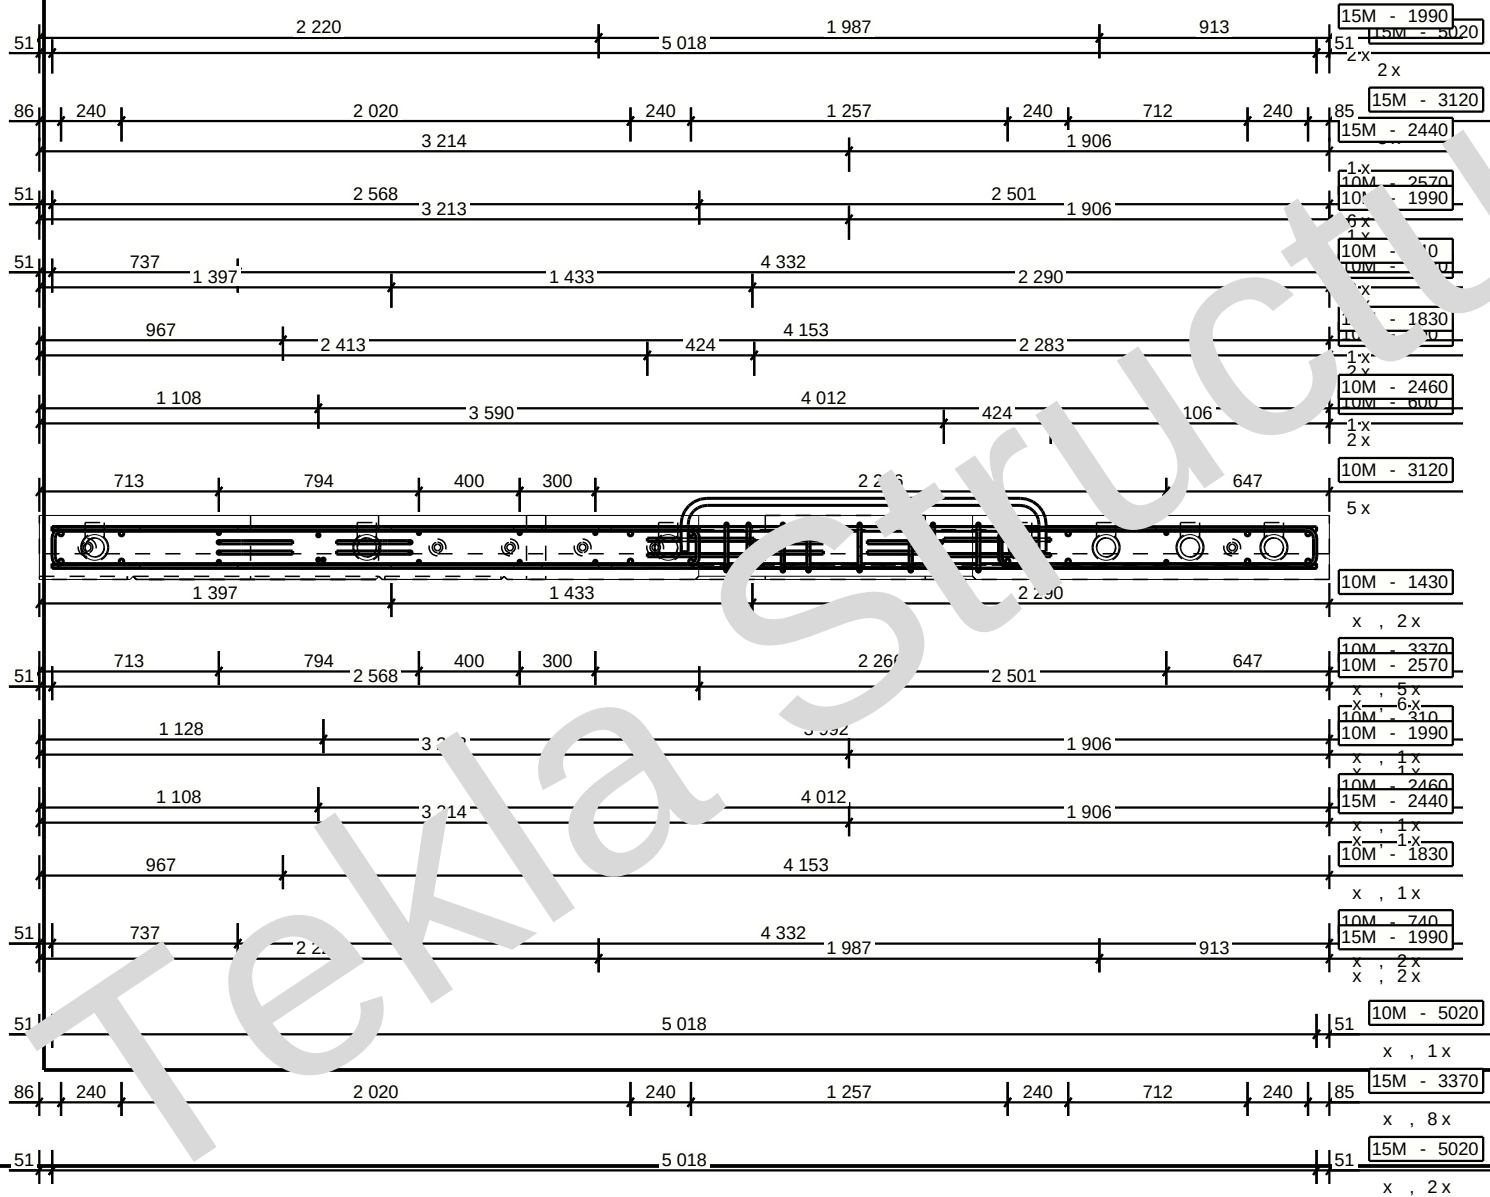

VIEW END 2
1:30

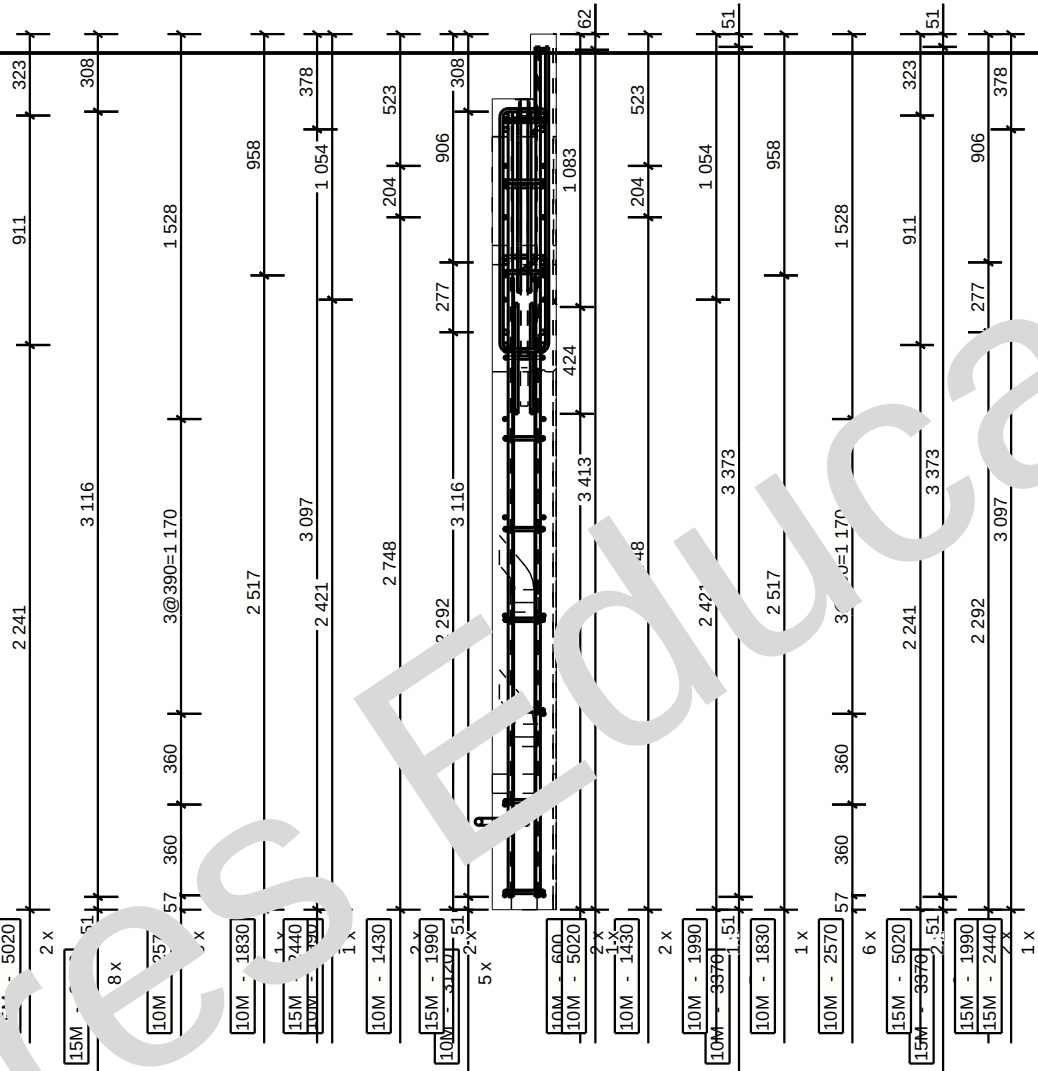

VIEW A
1:30

MIN. COVER				25 mm
BILL OF MATERIALS				
MARK	QTY.	DESCRIPTION	LENGTH	AREA
RB10M 000	4	10M - 11	2590	
RB10M 006	4	10M - 11	1280	
10M 000	4	10M - 14	1170	
RB10M 007	10	10M - TS67_2	3150	
RB10M 0074	4	10M - 14	1100	
RB10M 0048	17	10M - 17	800	
15M 0138	1	25M - 17	1740	
	1	10M - STR	310	
	4	10M - STR	600	
	4	10M - STR	740	
	4	10M - STR	1430	
	2	10M - STR	1830	
	2	10M - STR	1990	
	2	10M - STR	2460	
	12	10M - STR	2570	
	5	10M - STR	3120	
	5	10M - STR	3370	
	1	10M - STR	5020	
	4	15M - STR	1990	
	2	15M - STR	2440	
	8	15M - STR	3120	
	8	15M - STR	3370	
	4	15M - STR	5020	

STUBBE'S PRECAST			
PROJECT:			
PAISLEY TOWER			
PROJECT CODE:	PAINT CODE:	UNITS REQD.: 1	
DRAWN BY:	DATE:	SCALE: AS SHOWN	
ENGINEER:	DATE:	FILE:	
PROJECT No: P22-132		PIECE MARK: W10-78 PAGE - 2	