

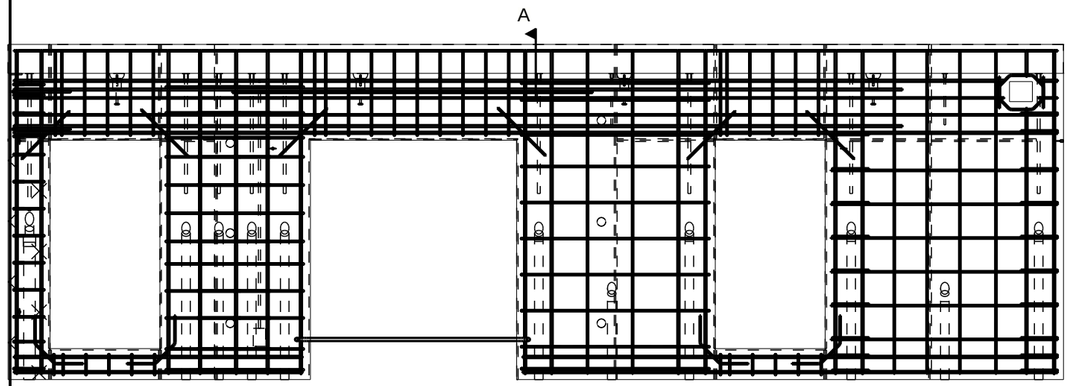


TOP IN FORM
1:50

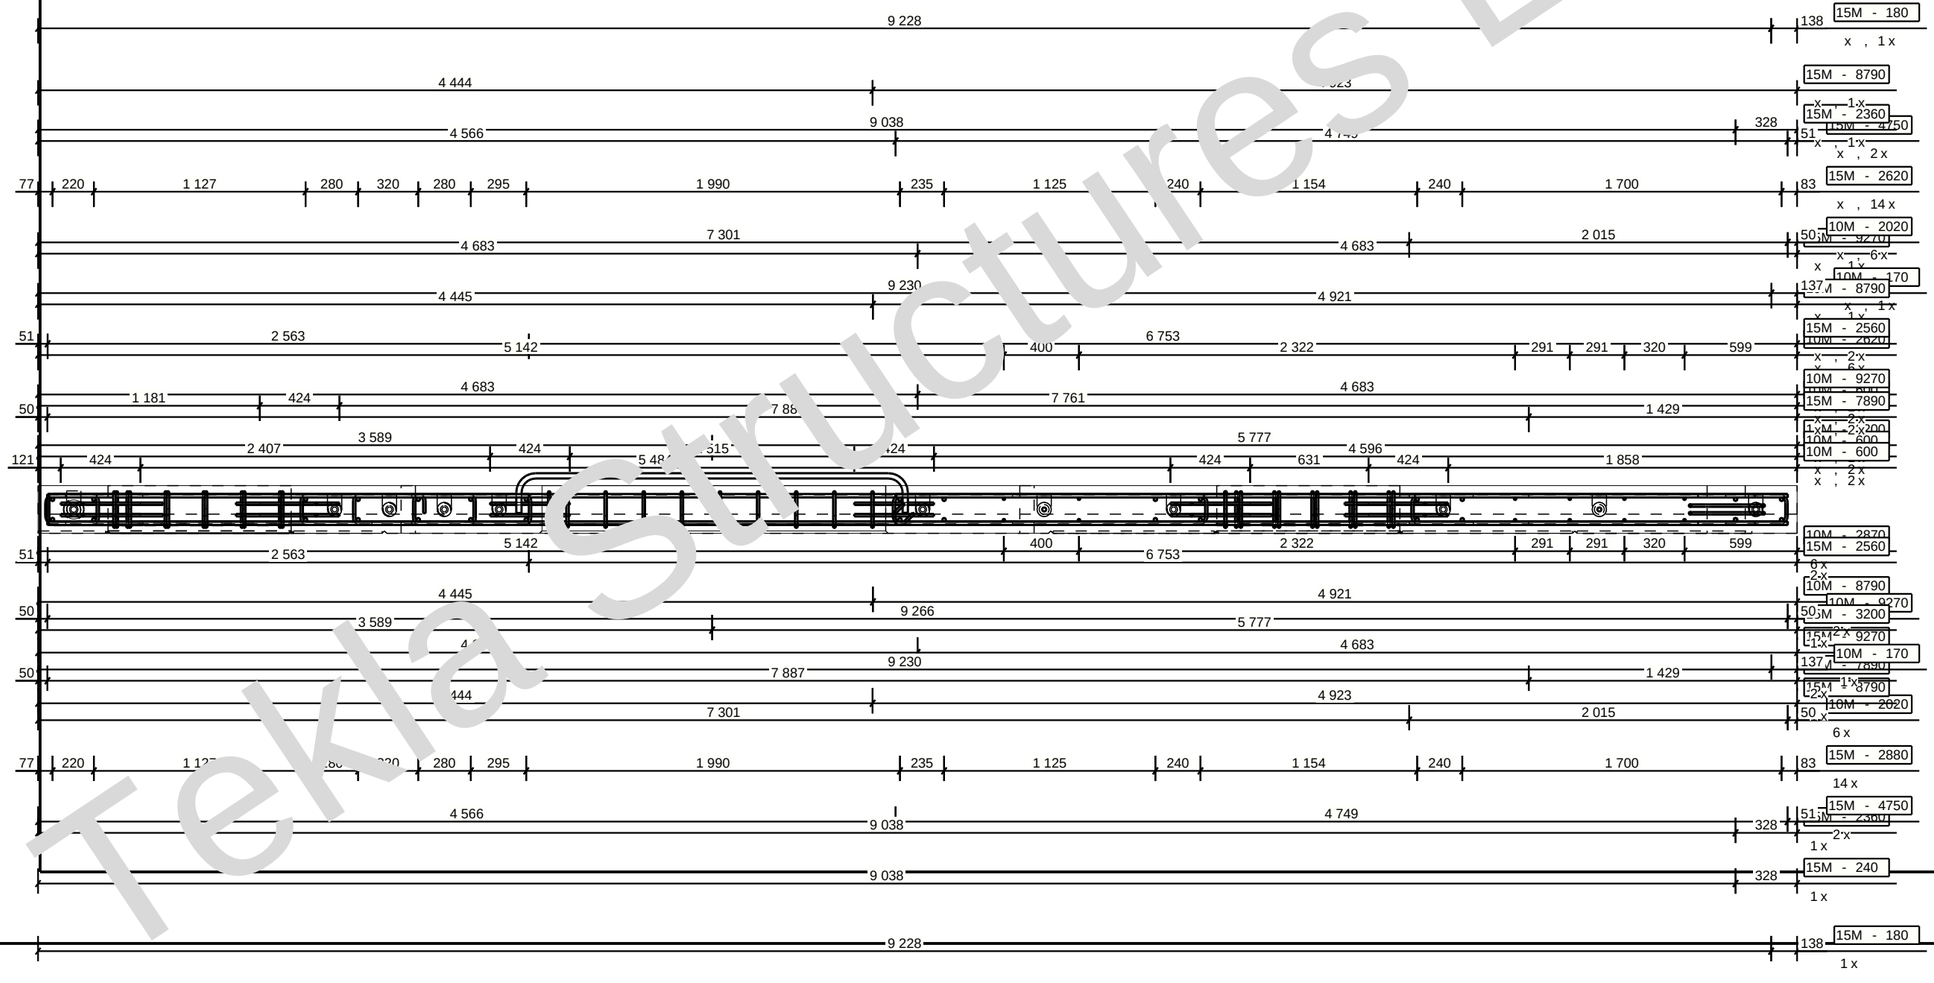

VIEW END 2
1:30

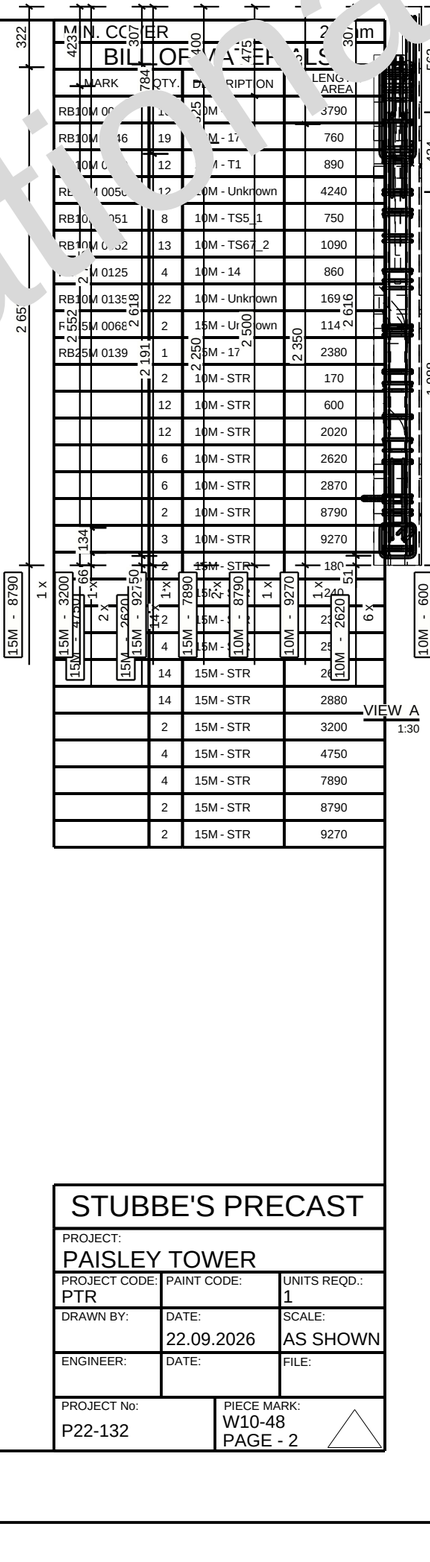

STUBBE'S PRECAST		
PROJECT: PAISLEY TOWER		
PROJECT CODE: PTR	PAINT CODE:	UNITS REQD.: 1
DRAWN BY:	DATE: 22.09.2026	SCALE: AS SHOWN
ENGINEER:	DATE:	FILE:
PROJECT No: P22-132	PIECE MARK: W10-48 PAGE - 2	

Tekla structures

Tekla Structures Educational