
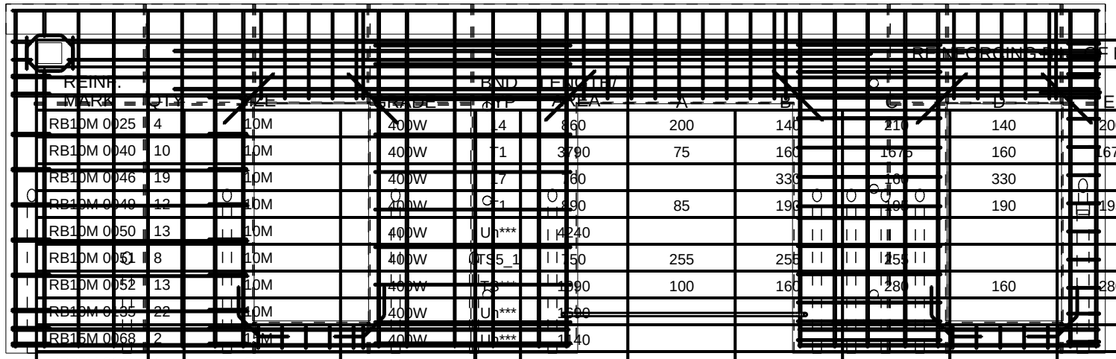



BAR BENDING SCHEDULE OF MATERIALS

REINF. MARK	QTY	SIZE	GRADE	END TYP	END FIN/HV AREA	A	B	C	D	E	F	G	H	H2	J	K	K2	O	PIN DIA.
RB10M 0025	4	10M	400W	14	360	200	140	210	140	200			100	100				405	
RB10M 0040	10	10M	400W	T1	3790	75	160	1675	160	1675		75							60
RB10M 0046	19	10M	400W	17	760		330	100	330										60
RB10M 0049	12	10M	400W	T1	890	85	190	100	190	195		85							
RB10M 0050	13	10M	400W	Un***	4240														
RB10M 0051	8	10M	400W	TS5_1	750	255	255	155											60
RB10M 0052	13	10M	400W	TS6***	1990	100	160	280	160	280	160	100							40
RB10M 0135	22	10M	400W	Un***	1680														
RB15M 0068	2	15M	400W	Un***	1140														
RB25M 0141	1	25M	400W	17	2380		210	2090	210										150
	2	10M	400W	STR	170		170												
	12	10M	400W	STR	600		600												
	12	10M	400W	STR	2020		2020												
	6	10M	400W	STR	2620		2620												
	6	10M	400W	STR	2870		2870												
	2	10M	400W	STR	8790		8790												
	3	10M	400W	STR	9270		9270												
	2	15M	400W	STR	170		170												
	1	15M	400W	STR	230		230												
	2	15M	400W	STR	2370		2370												
	4	15M	400W	STR	2560		2560												
	14	15M	400W	STR	2620		2620												
	14	15M	400W	STR	2880		2880												
	2	15M	400W	STR	3200		3200												
	4	15M	400W	STR	4750		4750												
	4	15M	400W	STR	7890		7890												
	2	15M	400W	STR	8790		8790												
	2	15M	400W	STR	9270		9270												


TOP IN FORM 1:48

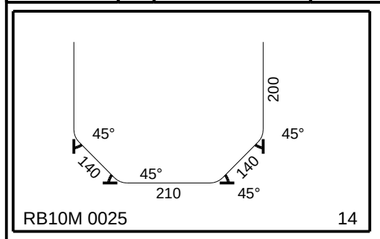


RB10M 0025 14

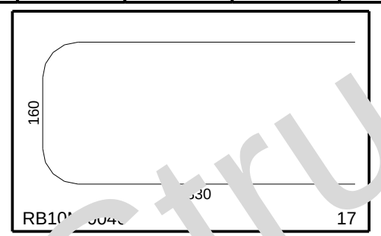


RB10M 0046 17

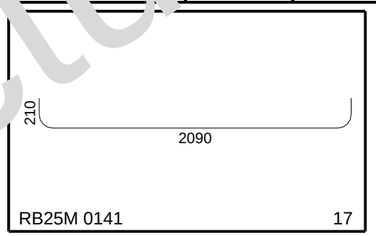


RB25M 0141 17

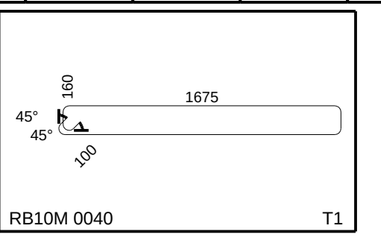


RB10M 0040 T1

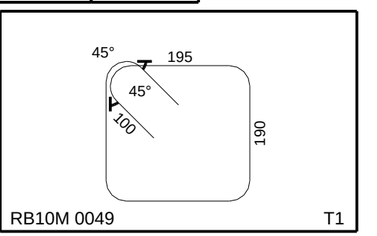


RB10M 0049 T1

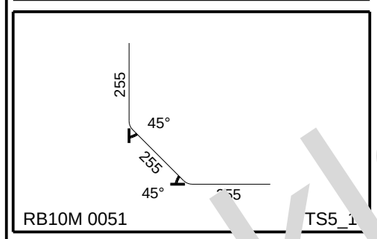


RB10M 0051 TS5_1

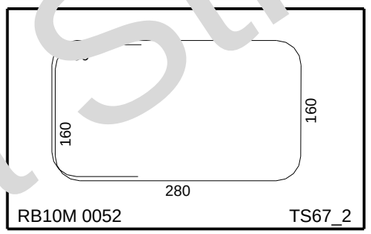


RB10M 0052 TS67_2

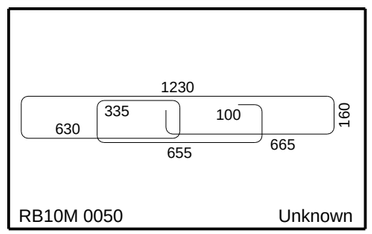

RB10M 0050 Unknown

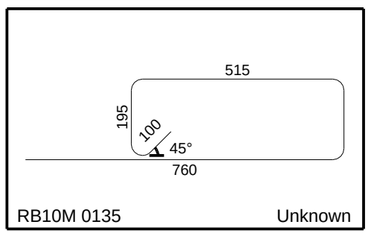

RB10M 0135 Unknown

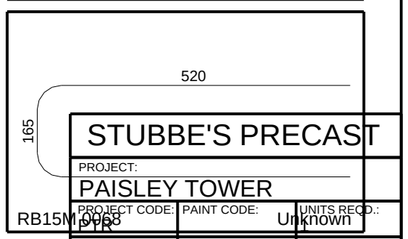

RB15M 0068 Unknown

STUBBE'S PRECAST	
PROJECT: PAISLEY TOWER	
PROJECT CODE: PTR	PAINT CODE: UNITS RECD.: Unknown
DRAWN BY:	DATE: 22.09.2026 SCALE: AS SHOWN
ENGINEER: NA	DATE: FILE:
PROJECT No: P22-132	PIECE MARK: W10-59 PAGE - 3

Tekla structures

Tekla Structures Educational