
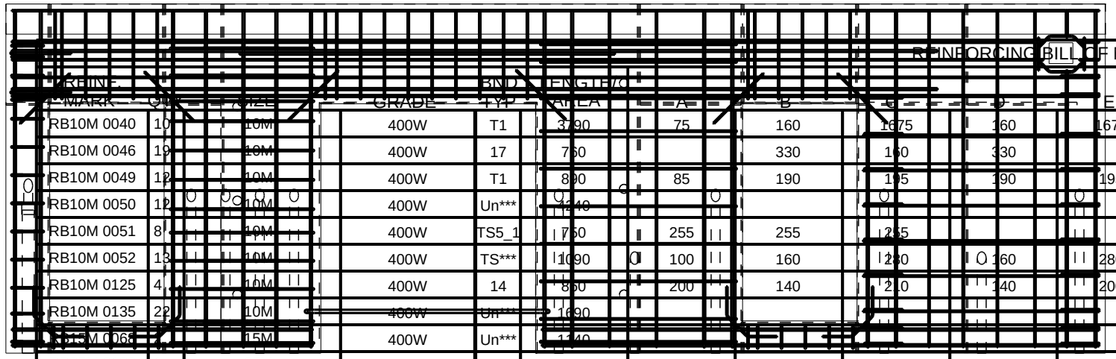


REINFORCING BILL OF MATERIALS


REINF MARK	QTY	SIZE	GRADE	BND TYP	LENGTH/ CAMBER	A	B	C	D	E	F	G	H	H2	J	K	K2	O	PIN DIA.	
RB10M 0040	10	10M	400W	T1	3790	75	160		1675	160	1675		75							
RB10M 0046	19	10M	400W	17	760		330		160	330										60
RB10M 0049	12	10M	400W	T1	890	85	190		195	190	195		85							40
RB10M 0050	12	10M	400W	Un***	1340															
RB10M 0051	8	10M	400W	TS5_1	750	255	255		255	255										60
RB10M 0052	13	10M	400W	TS***	1090	100	160		280	160	280	160	100							40
RB10M 0125	4	10M	400W	14	860	200	140		210	140	200			100	100				405	60
RB10M 0135	22	10M	400W	Un***	1690															
RB10M 0068	1	15M	400W	Un***	1140															
RB25M 0139	1	25M	400W	17	2380		210		2085	210										150
	2	10M	400W	STR	170		170													
	12	10M	400W	STR	600		600													
	12	10M	400W	STR	2020		2020													
	6	10M	400W	STR	2620		2620													
	6	10M	400W	STR	2870		2870													
	2	10M	400W	STR	8790		8790													
	3	10M	400W	STR	9270		9270													
	2	15M	400W	STR	180		180													
	1	15M	400W	STR	240		240													
	2	15M	400W	STR	2360		2360													
	4	15M	400W	STR	2560		2560													
	14	15M	400W	STR	2620		2620													
	14	15M	400W	STR	2880		2880													
	2	15M	400W	STR	3200		3200													
	4	15M	400W	STR	4750		4750													
	4	15M	400W	STR	7890		7890													
	2	15M	400W	STR	8790		8790													
	2	15M	400W	STR	9270		9270													

TOP IN FORM


1:48

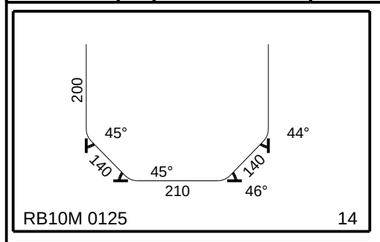


RB10M 0125 14

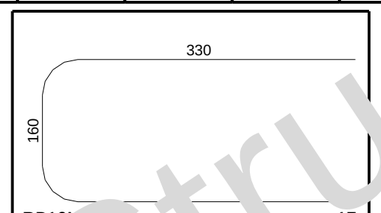


RB10M 0040 17

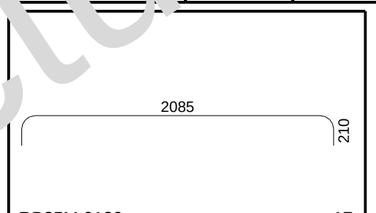


RB25M 0139 17

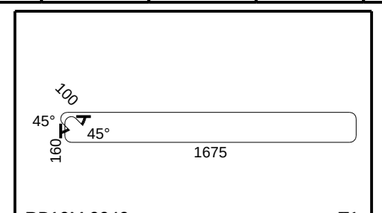


RB10M 0040 T1

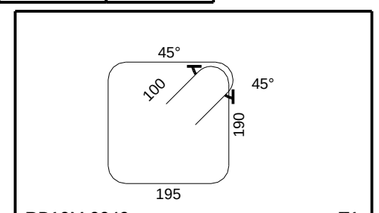


RB10M 0049 T1

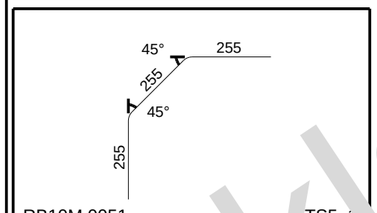


RB10M 0051 TS5_1

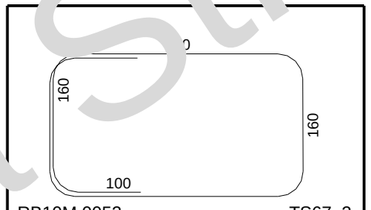


RB10M 0052 TS67_2

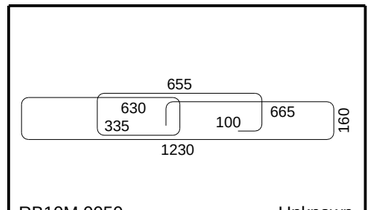

RB10M 0050 Unknown

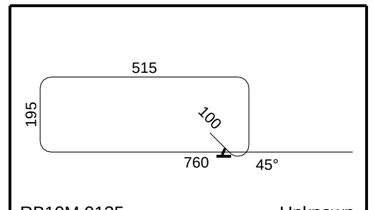

RB10M 0135 Unknown

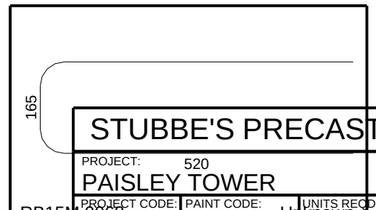

RB15M 0068

STUBBE'S PRECAST		
PROJECT: PAISLEY TOWER		
PROJECT CODE: PTR	PAINT CODE:	UNITS RECD.: Unknown
DRAWN BY:	DATE: 22.09.2026	SCALE: AS SHOWN
ENGINEER: NA	DATE:	FILE:
PROJECT No: P22-132	PIECE MARK: W10-71 PAGE - 3	

Tekla structures

Tekla Structures Education